

# SHWETA PAUL VERMA

Experience Portfolio

[www.shwetapaul.com](http://www.shwetapaul.com)



## OBJECTIVE

Seeking a uniquely creative and client-driven design position which distinctively set itself apart from other jobs as it sparked excitement for initial planning and design development with a focus in spatial relations and exploring new work trends.



# WELCOME TO MY CREATIVE PORTFOLIO





*Hello, my name is....*

# SHWETA PAUL VERMA

A creative, passionate & proactive interior designer with more than 11+ years of design experience in several sectors like residential, commercial, mixed use & planning from several organizations in India and UAE. Being highly career driven and a very motivated designer with good communication and problem solving skills, my goal is to deliver high quality interiors while personally enhancing my skills to be a project lead.



---

• CREATIVE

• INNOVATIVE

• PRODUCTIVE

• COOPERATIVE

---

# VISION

My aim to shape spaces with “timeless designs” and want to be recognized as **professional interior designer & asset** to the company, providing solutions in the field of high-end corporate, commercial & residential interiors.

---


# MISSION

**My mission** is to positively influence the lives of all colleagues & customers with whom we have the pleasure of working, & leave a lasting impression on their minds and **imagination**. The designs must inspire and elevate the hearts and minds of all those who lay eyes on it. The long-term goals are always in line with our core values.





# PERSONAL SKILLS

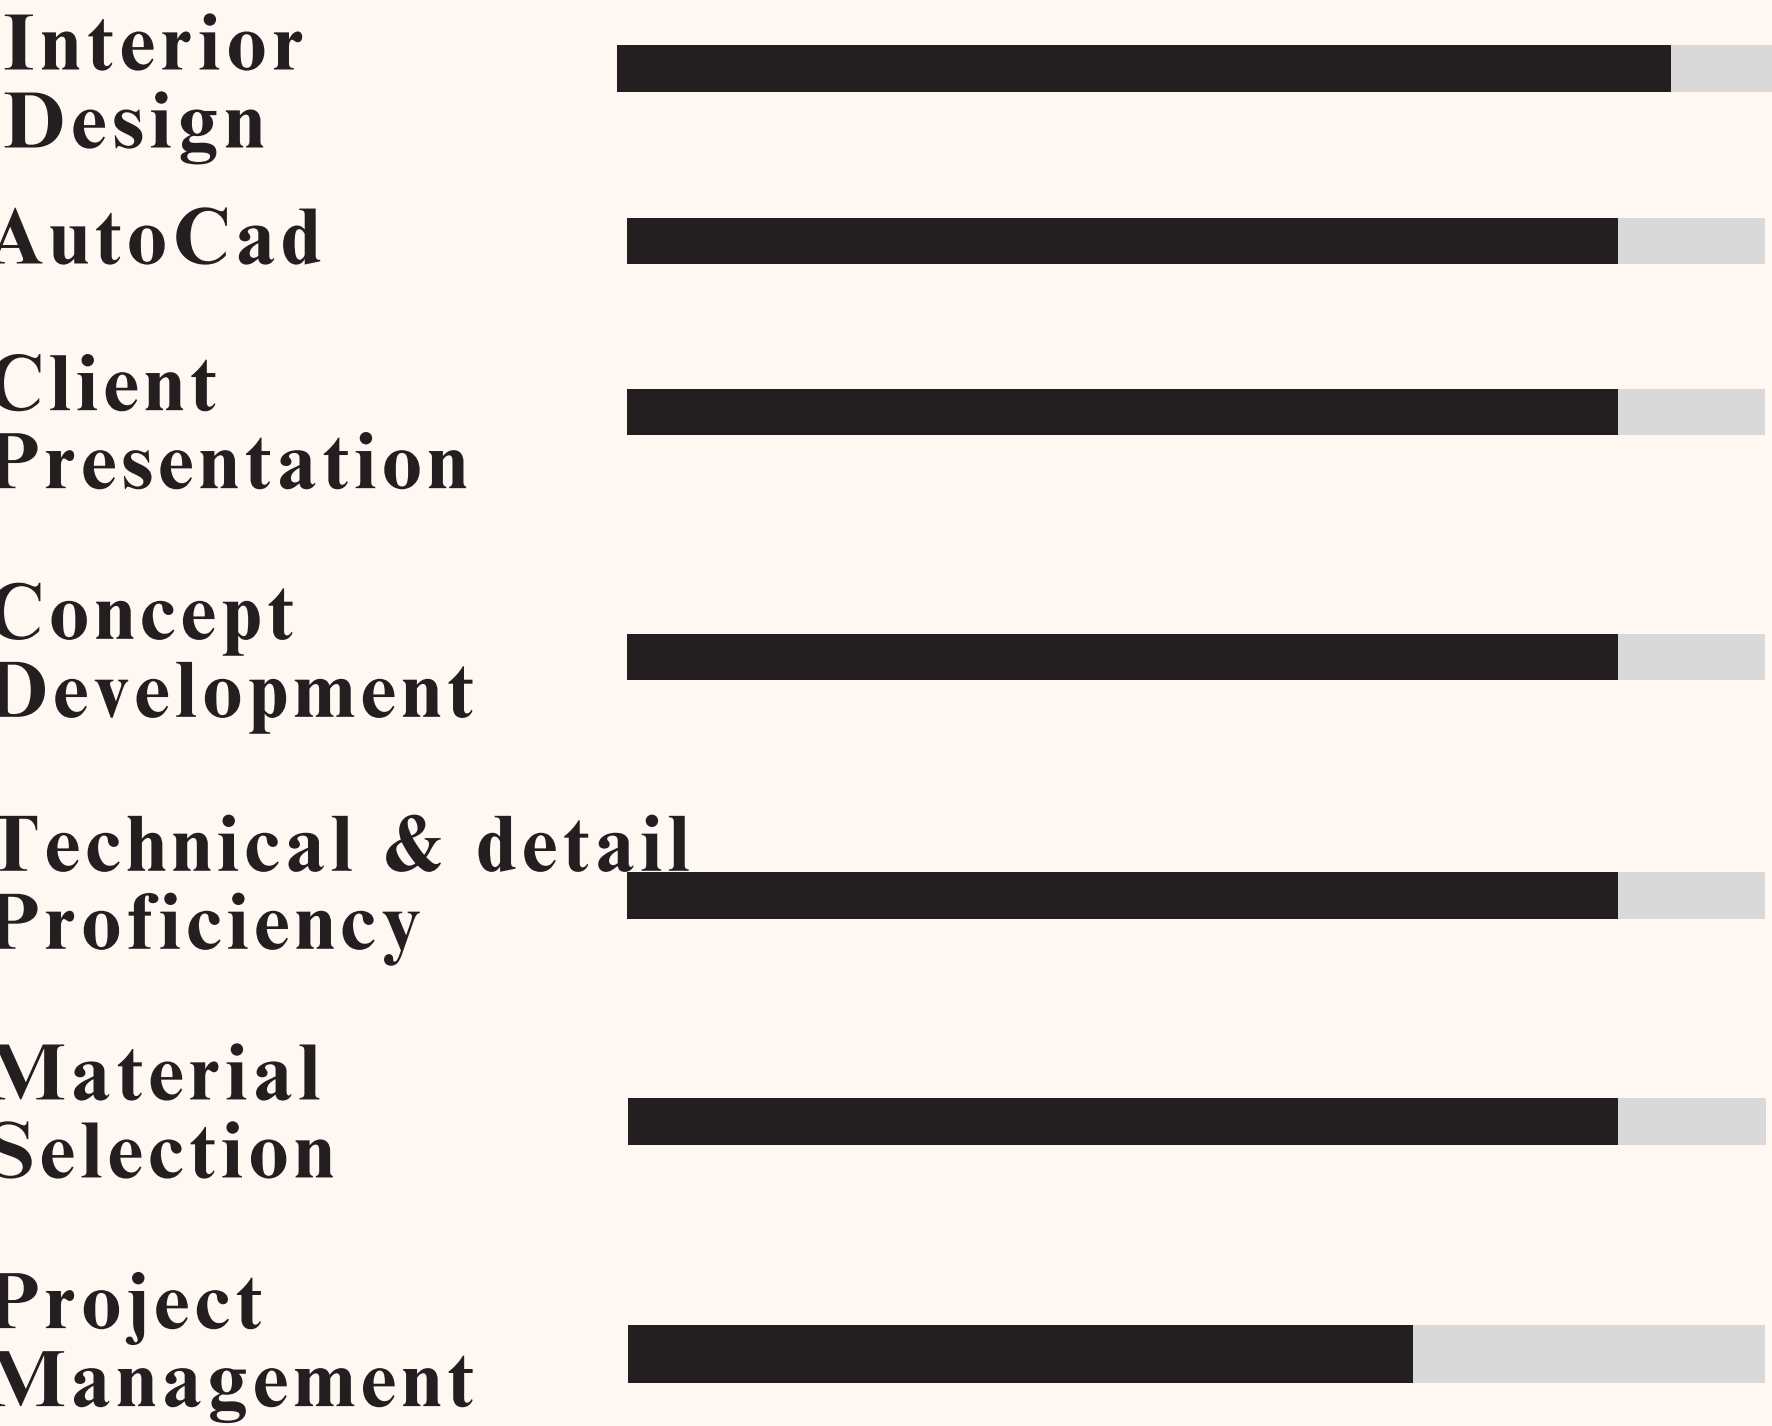

# ACADEMICS BACKGROUND







# WORK EXPERIENCE

- Vianaar Home pvt Ltd
- Studio Srijan
- Delta Faucet
- LineZ 'N' DesignZ
- Ankur & Associates



# NOTABLE PROJECT

- MAR LOUNGE
- APPLE TREE GARDEN
- VILLA 17
- AL AWADHI JEWELLERY
- REBOUND
- HANGER LET'S PADEL











GLIMPSE OF  
**Approved**  
**DRAWING**





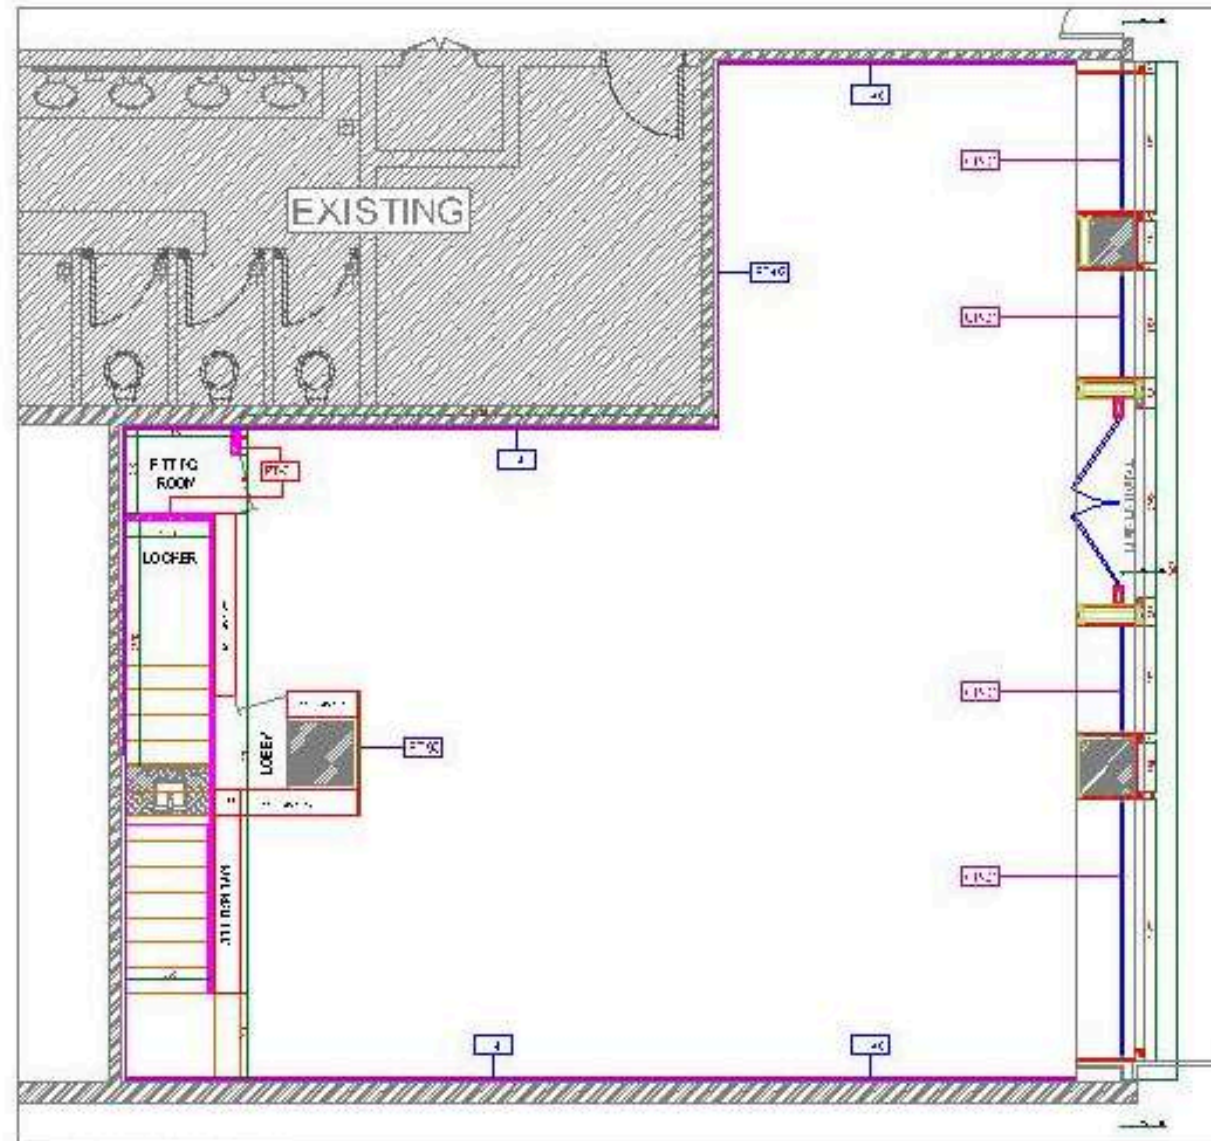


GROUND FLOOR  
PARTITION LAYOUT

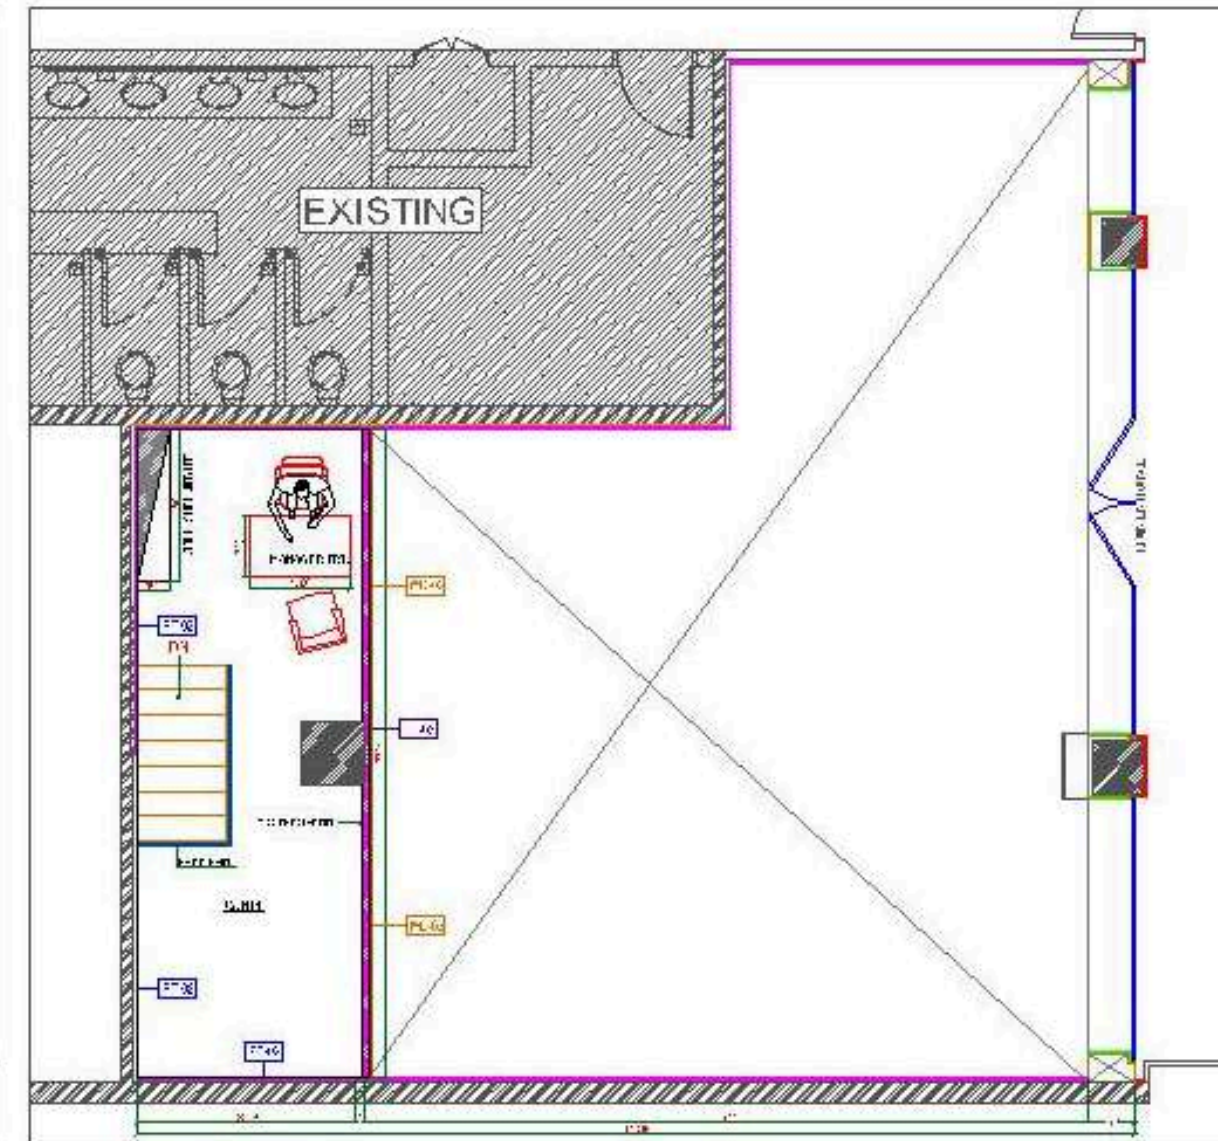


MEZZANINE FLOOR  
G. ARRANGEMENT LAYOUT

|       |                                                             |
|-------|-------------------------------------------------------------|
| PT-01 | 10cm GYPSUM WALL PARTITION                                  |
| PT-02 | 12mm THK. FIRE RATED GYPSUM WALL LINING                     |
| GP-01 | 12mm THK. CLEAR TEMPERED GLASS AS PER APPROVED SAMPLE       |
| WD-02 | 12mm THK. HDF BACKING WITH VENEER, F.N. SH. AS PER 3D VIEWS |
| PT-03 | HDF BACKING W/ TILE CLADDING AS PER 3D VIEWS                |



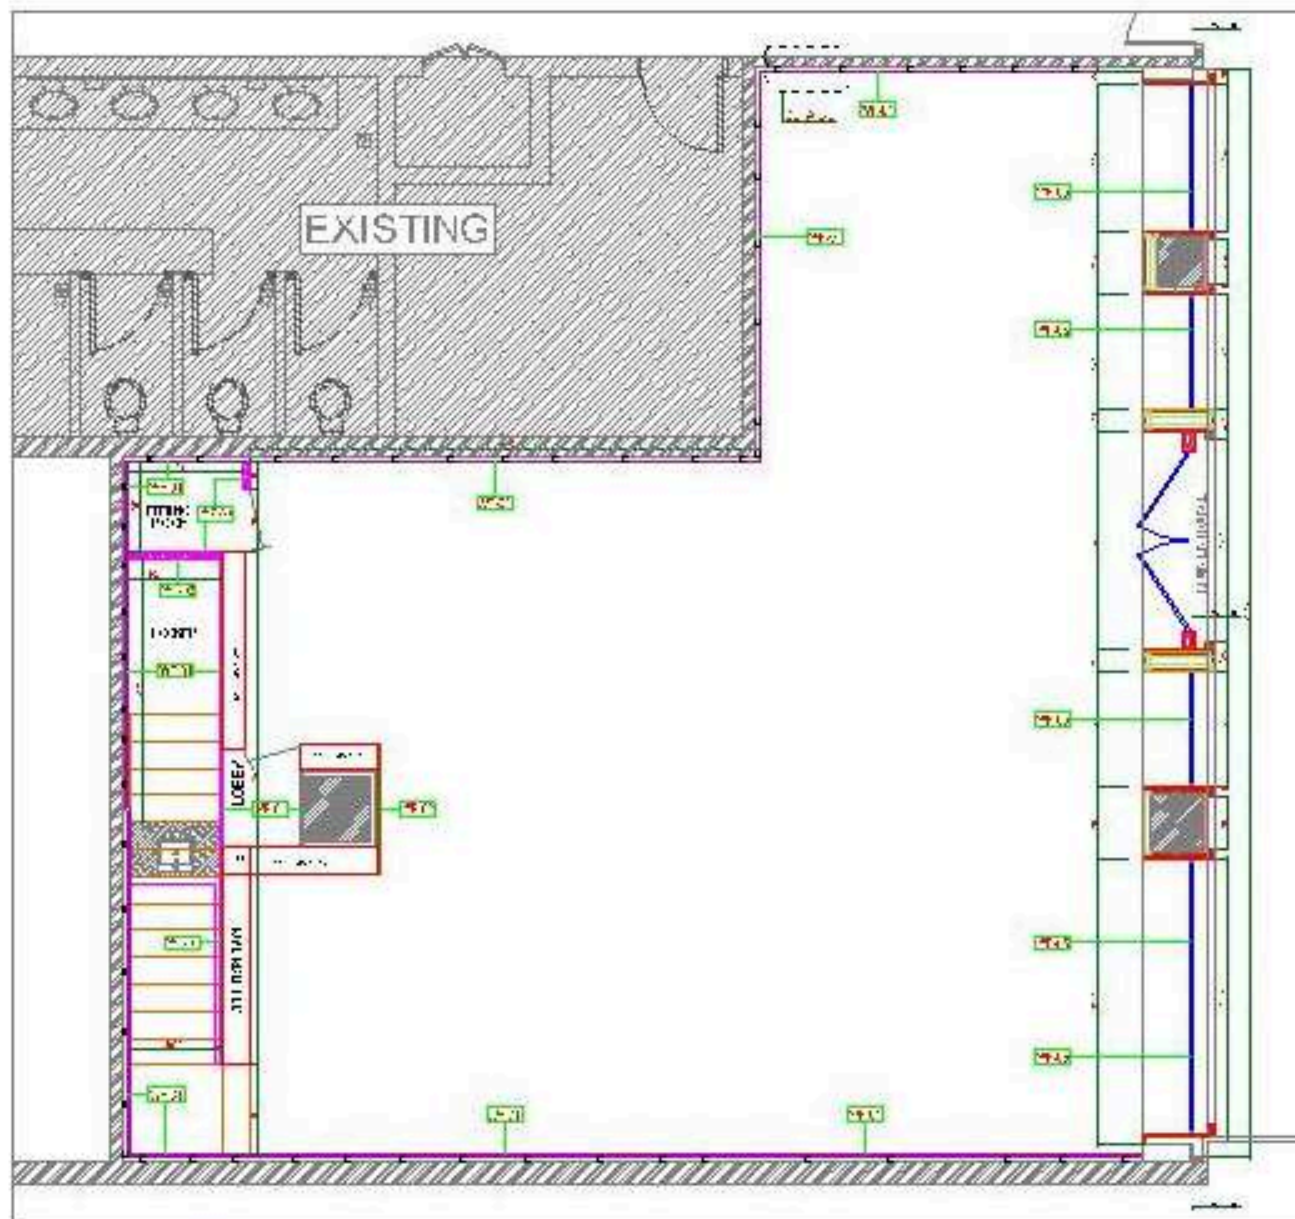


GROUND FLOOR  
WALL FINISHES LAYOUT

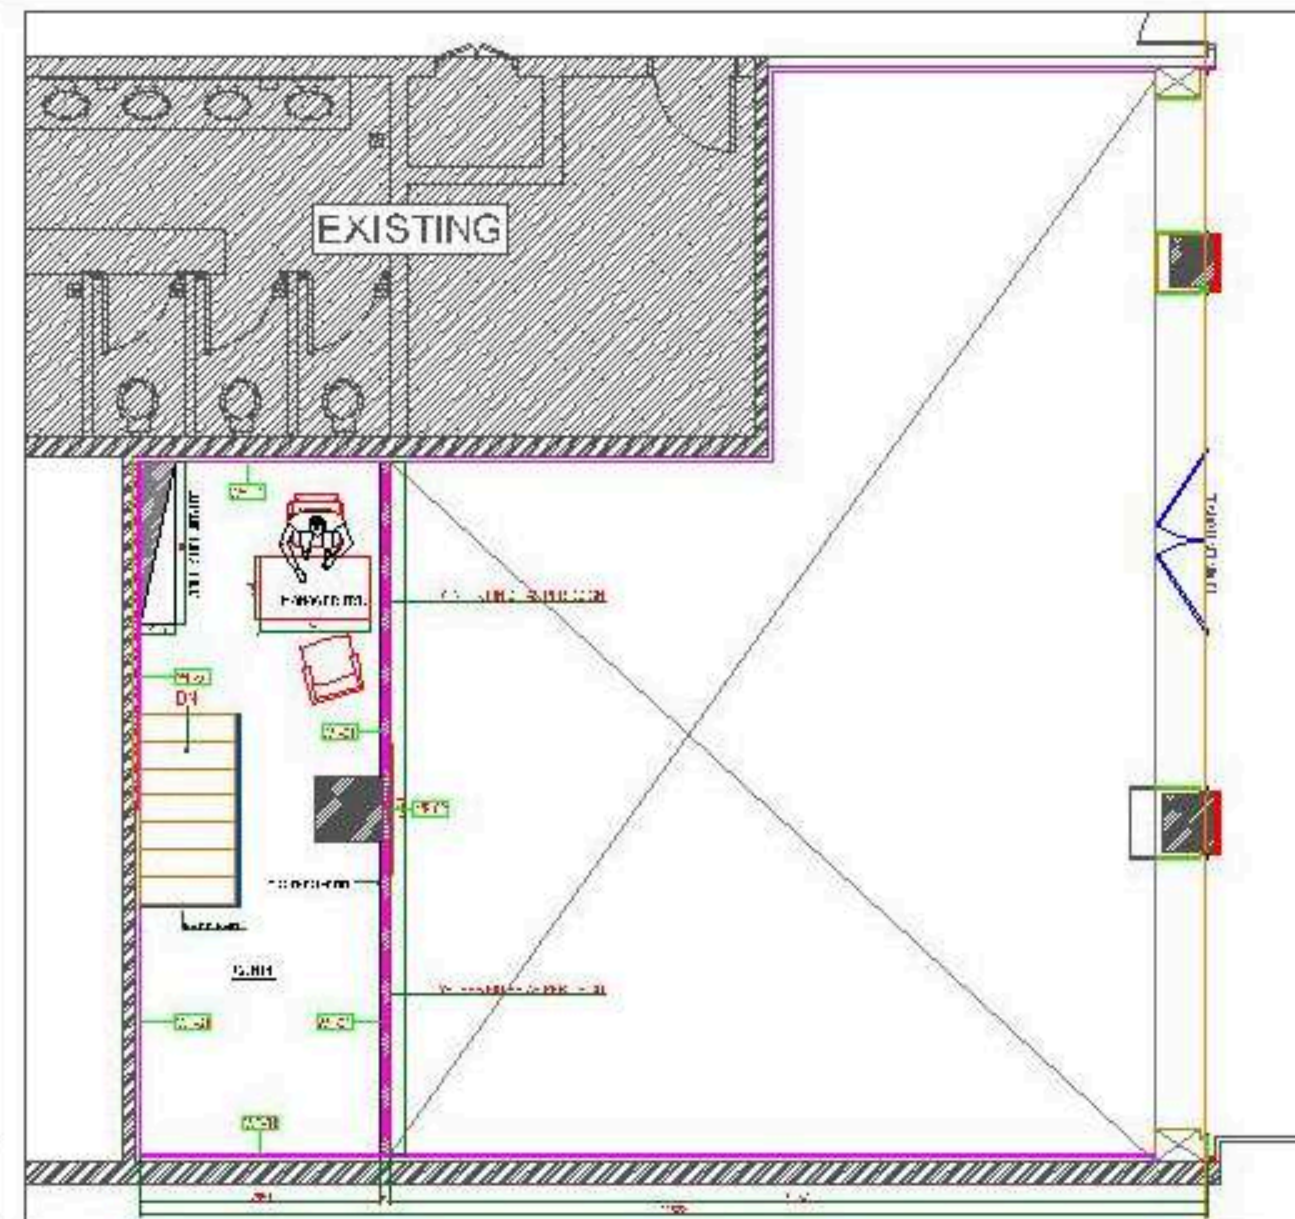


MEZZANINE FLOOR  
WALL FINISHES LAYOUT

|       |                                                      |
|-------|------------------------------------------------------|
| WF-01 | WHITE PAINT FINISH                                   |
| WF-02 | PORCELAIN WALL TILE FINISH AS PER APPROVED SAMPLE    |
| WF-03 | 10cm GYPSUM WALL PARTITION WITH WHITE PAINT FINISH   |
| WF-05 | 12mm THK CLEAR TEMPERED GLASS AS PER APPROVED SAMPLE |



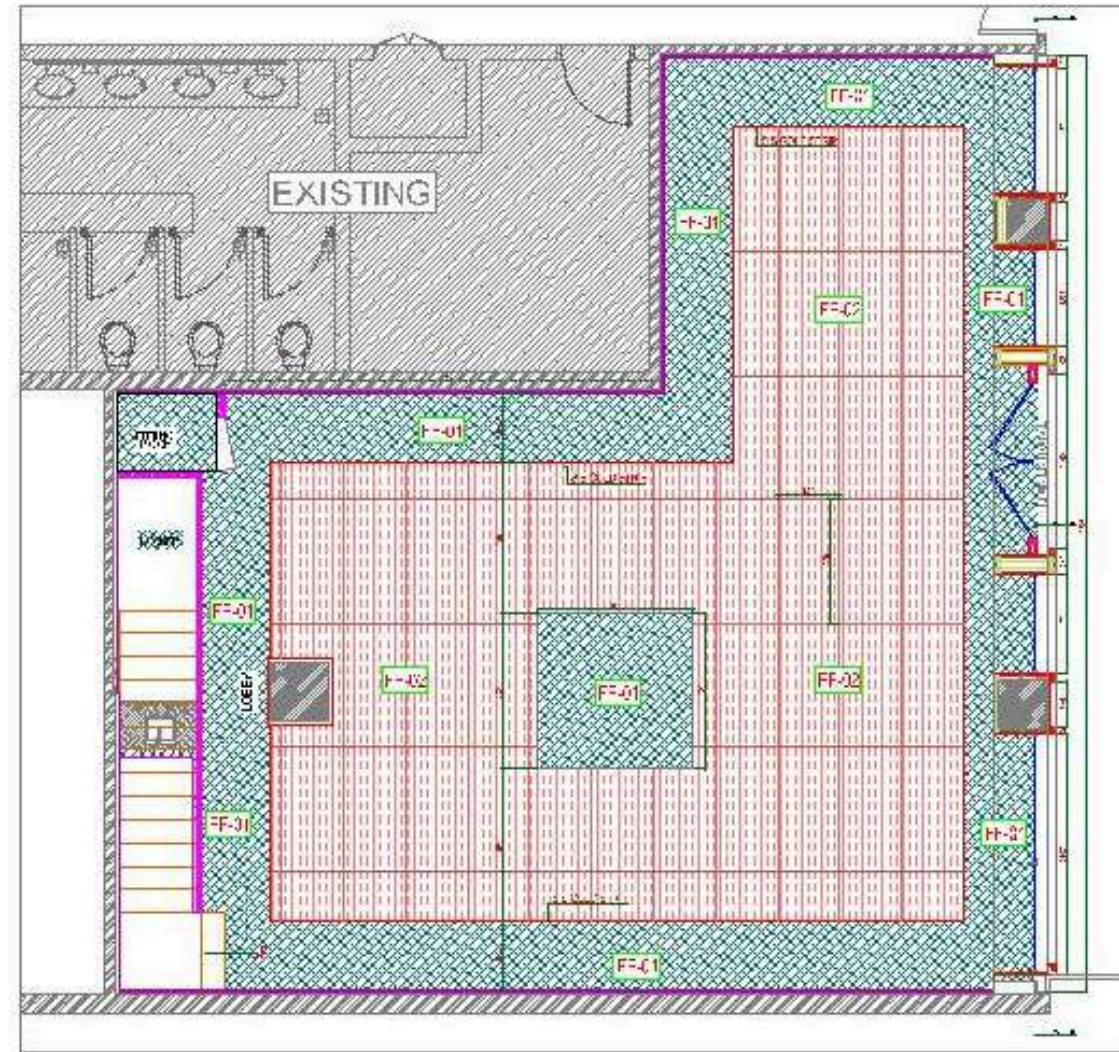


GROUND FLOOR  
FLOOR FINISHES LAYOUT

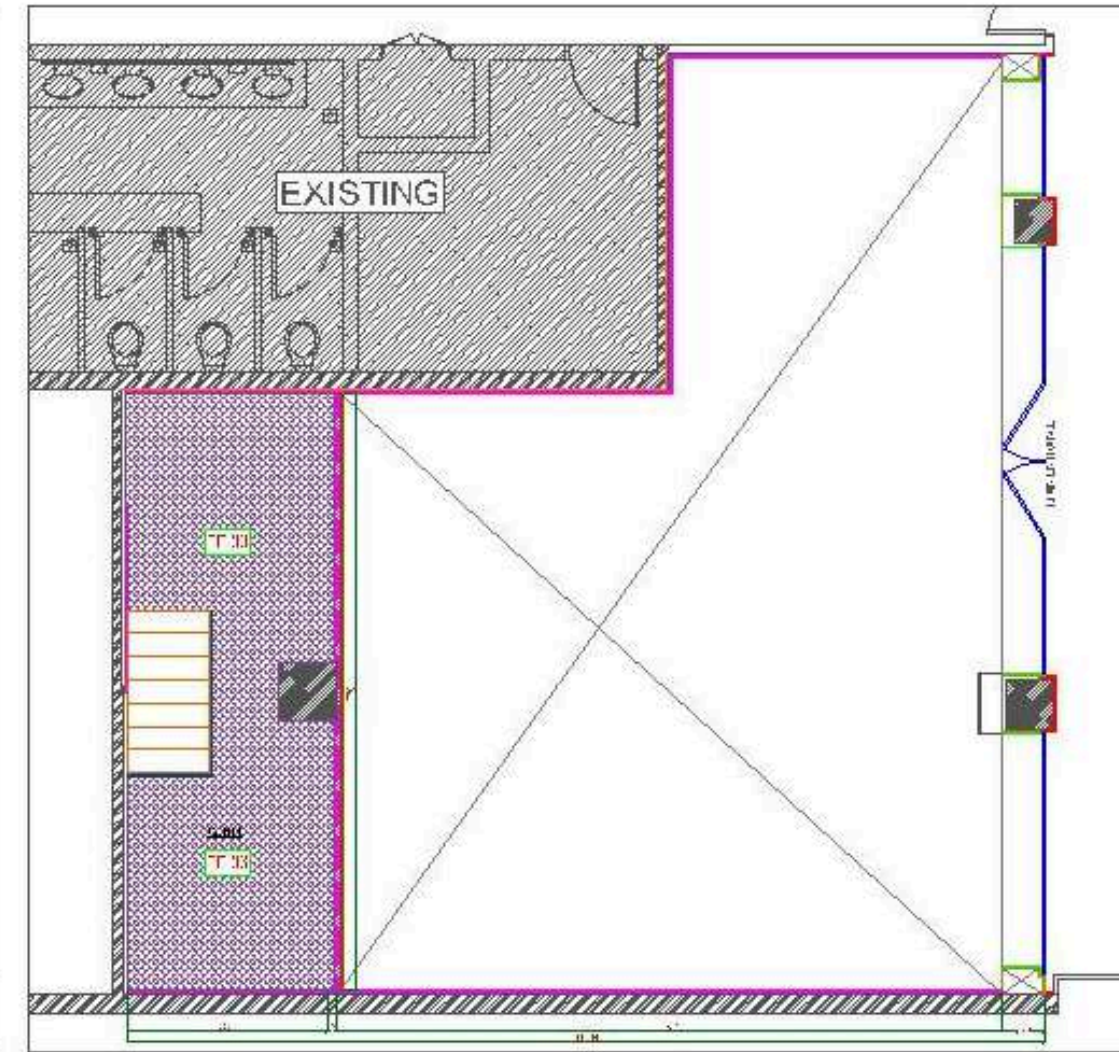


MEZZANINE FLOOR  
FLOOR FINISHES LAYOUT

|                                                                                     |                                                     |
|-------------------------------------------------------------------------------------|-----------------------------------------------------|
|  | BLACK MARQUINA TILE AS PER APPROVED SAMPLE          |
|  | 80' x1601mm GREY ARMANI TILE FINISH AS PER 3D VIEWS |
|  | CARPET FLOORING AS PER APPROVED SAMPLE              |

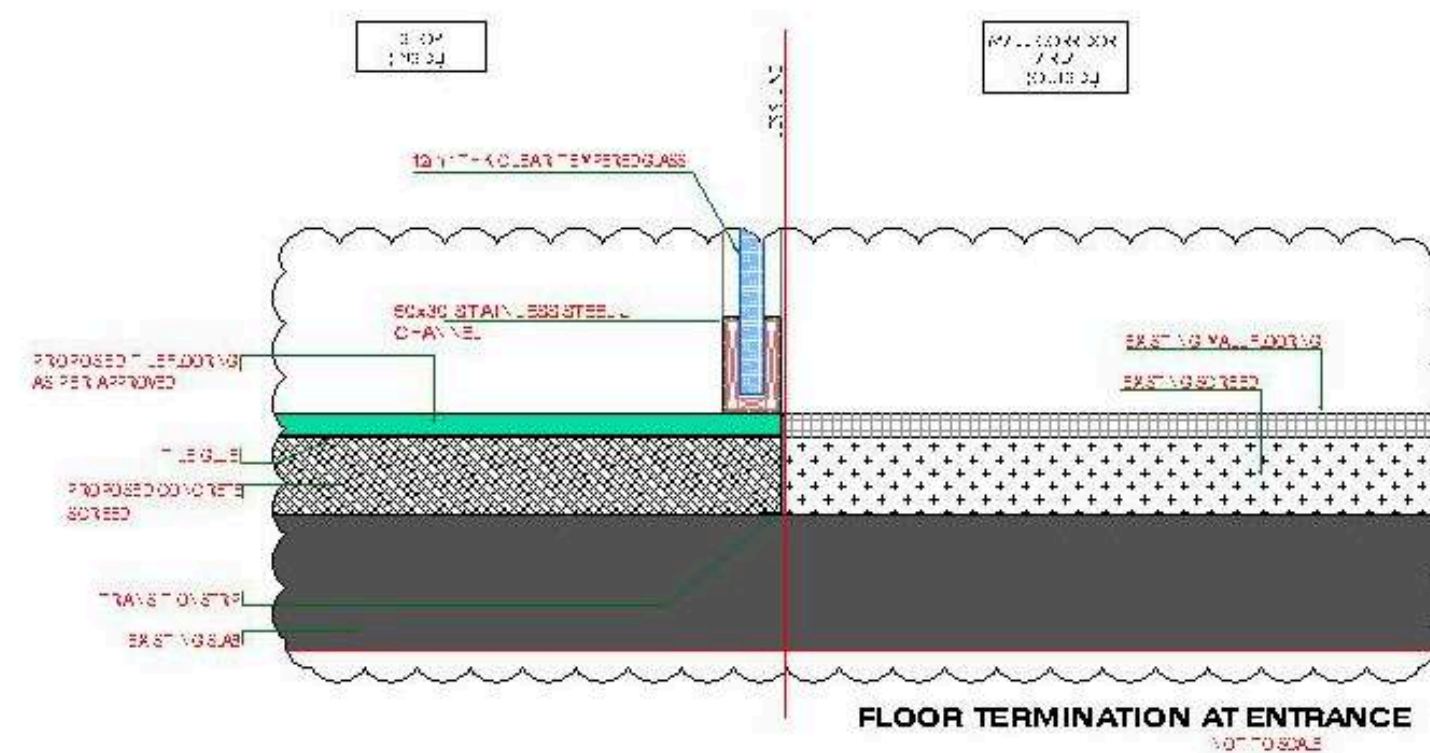


FLOOR TERMINATION AT ENTRANCE  
NOT TO SCALE





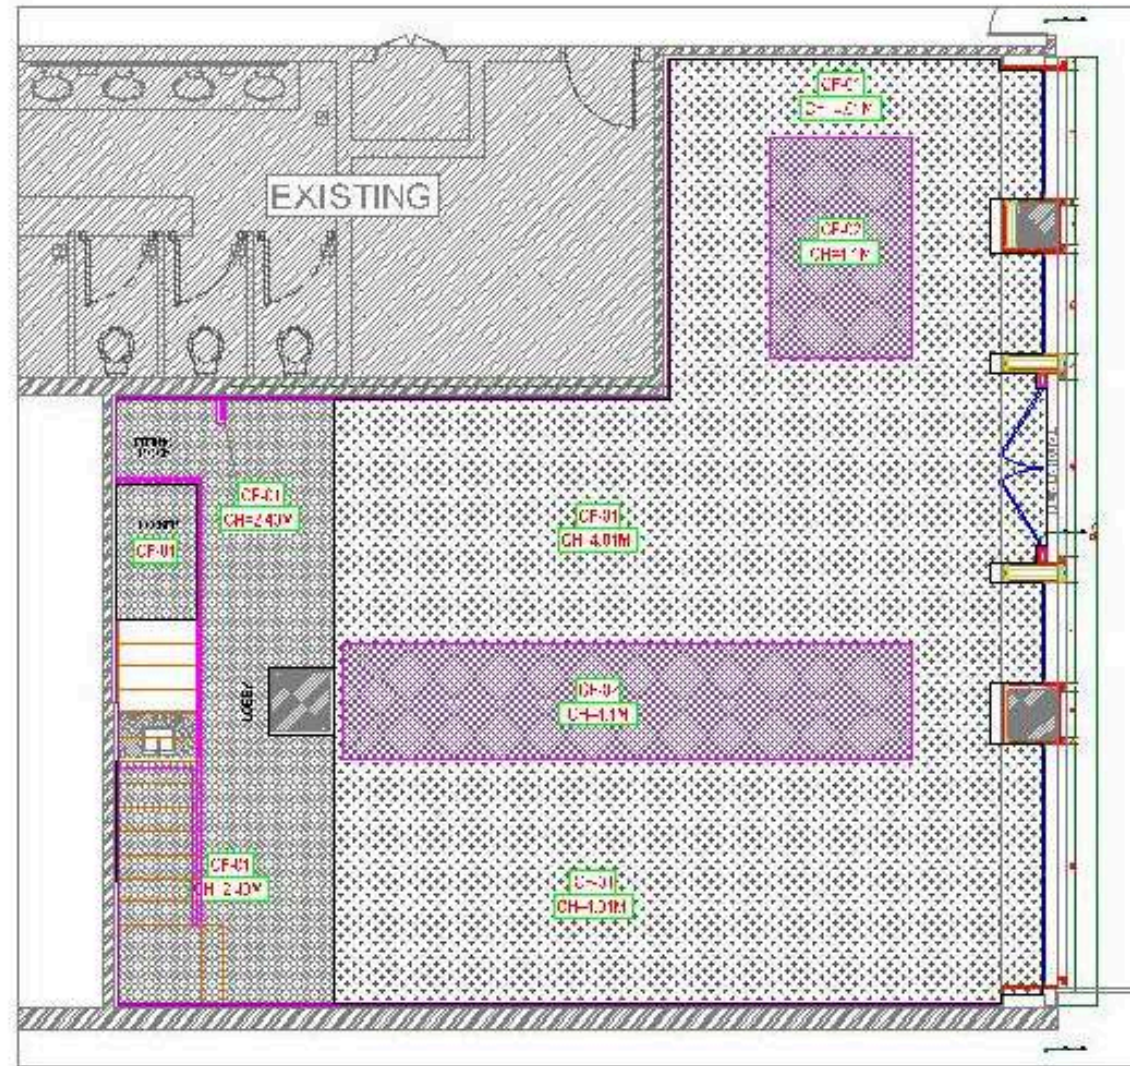


GROUND FLOOR  
CEILING FINISHES LAYOUT

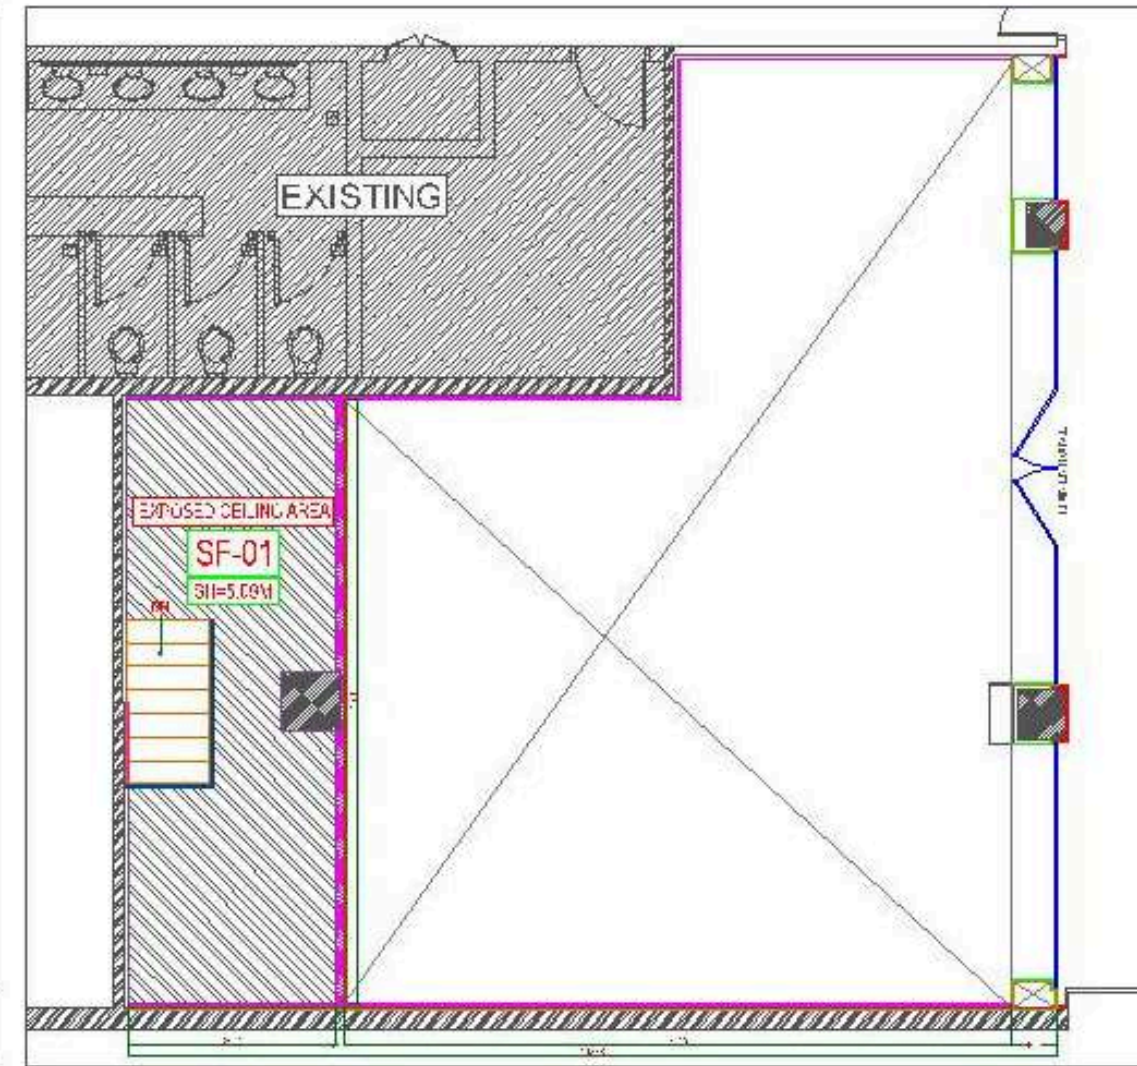


MEZZANINE FLOOR  
CEILING FINISHES LAYOUT
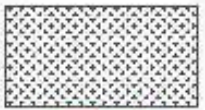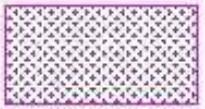
|                                                                                       |                                                           |
|---------------------------------------------------------------------------------------|-----------------------------------------------------------|
|  | GYPSUM CEILING WITH WHITE PAINT<br>FINISH AS PER 3D VIEWS |
|  | GYPSUM CEILING WITH CHANDELIER<br>AS PER 3D VIEWS         |
|  | GRAY PAINT FINISH ON EXPOSED<br>CEILING AREA              |




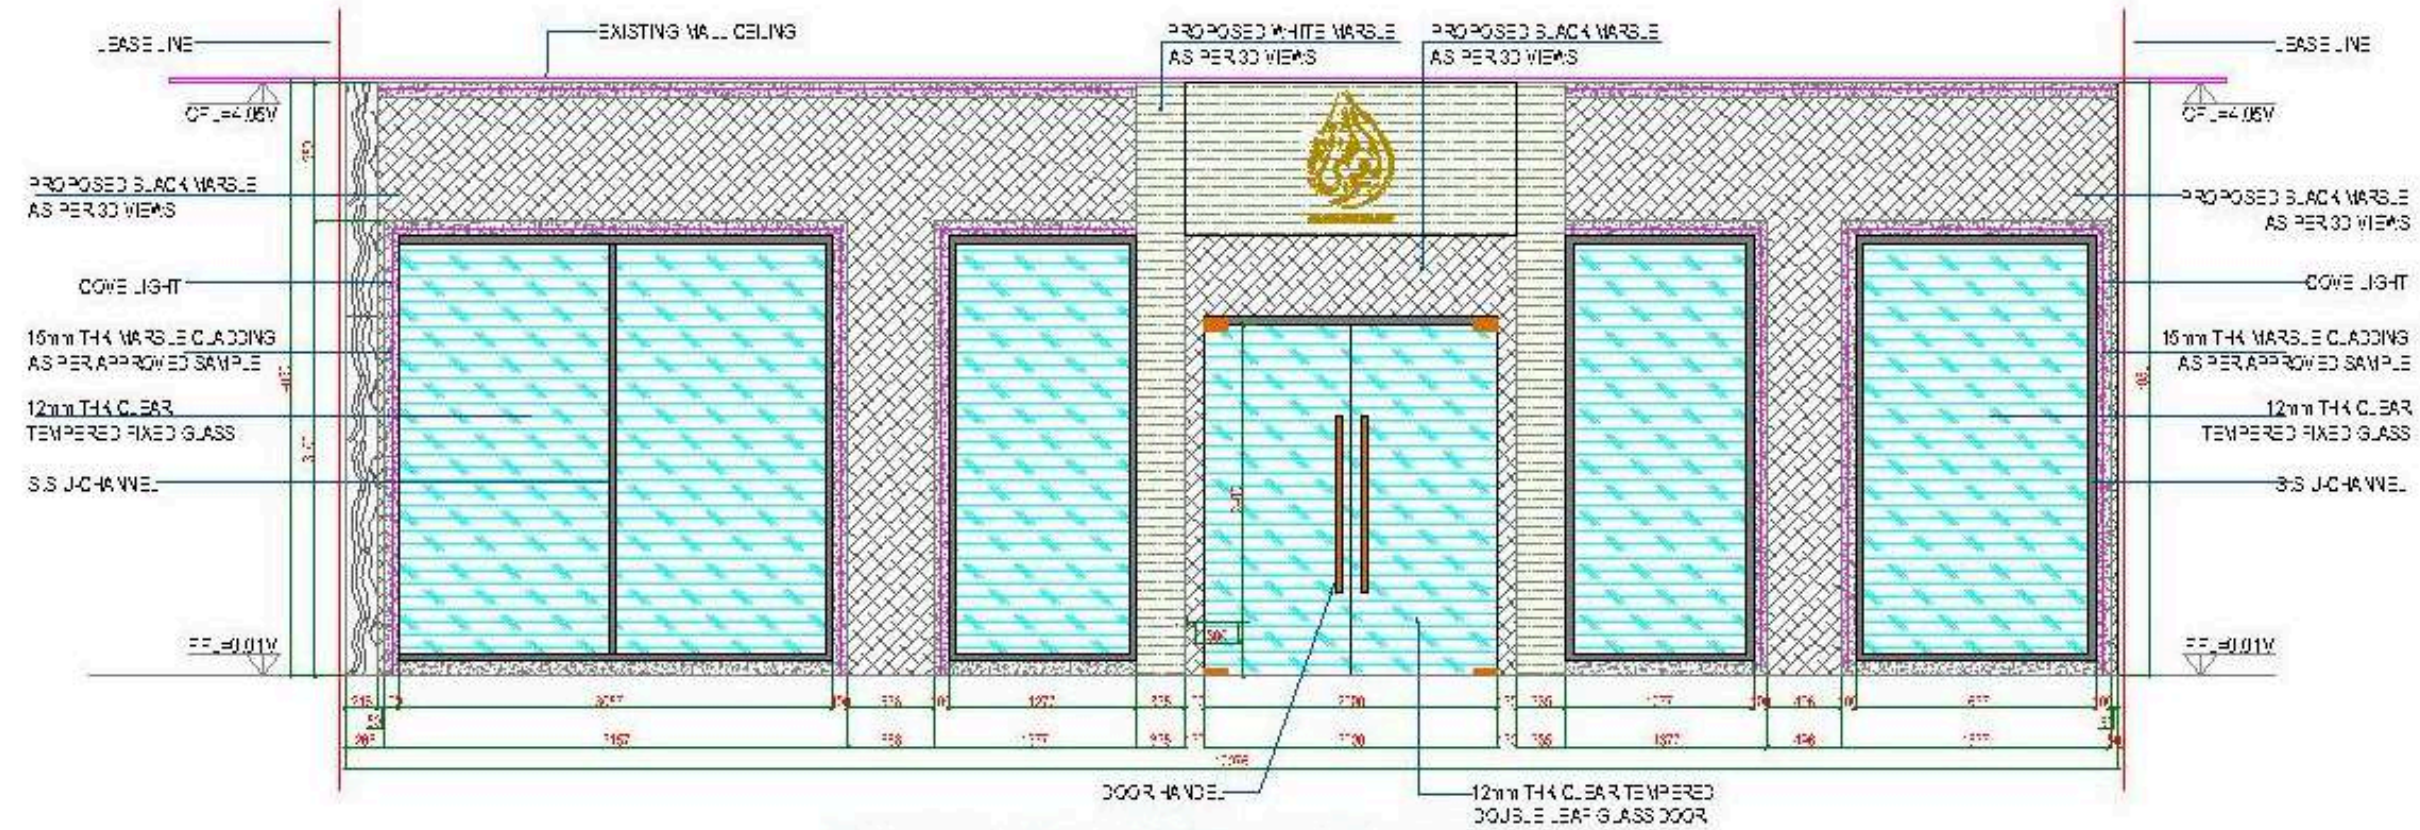


SHOP FRONT ELEVATION (A)

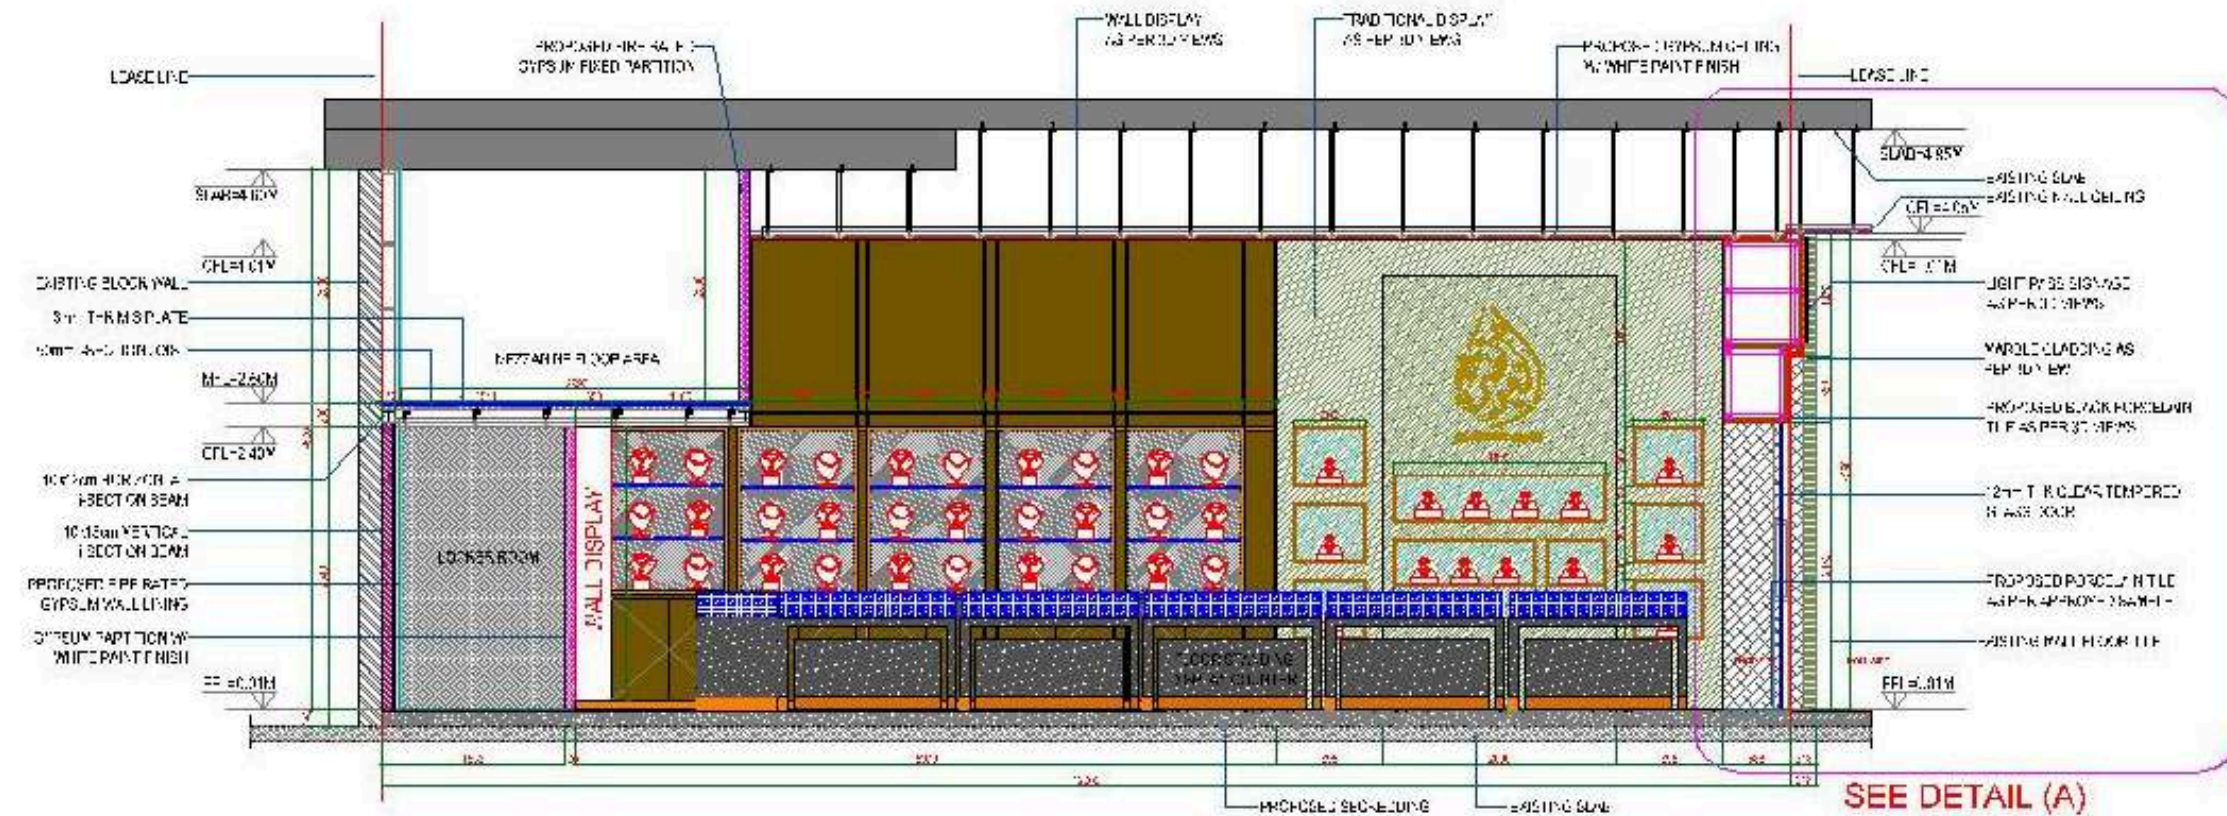

SECTION (A)



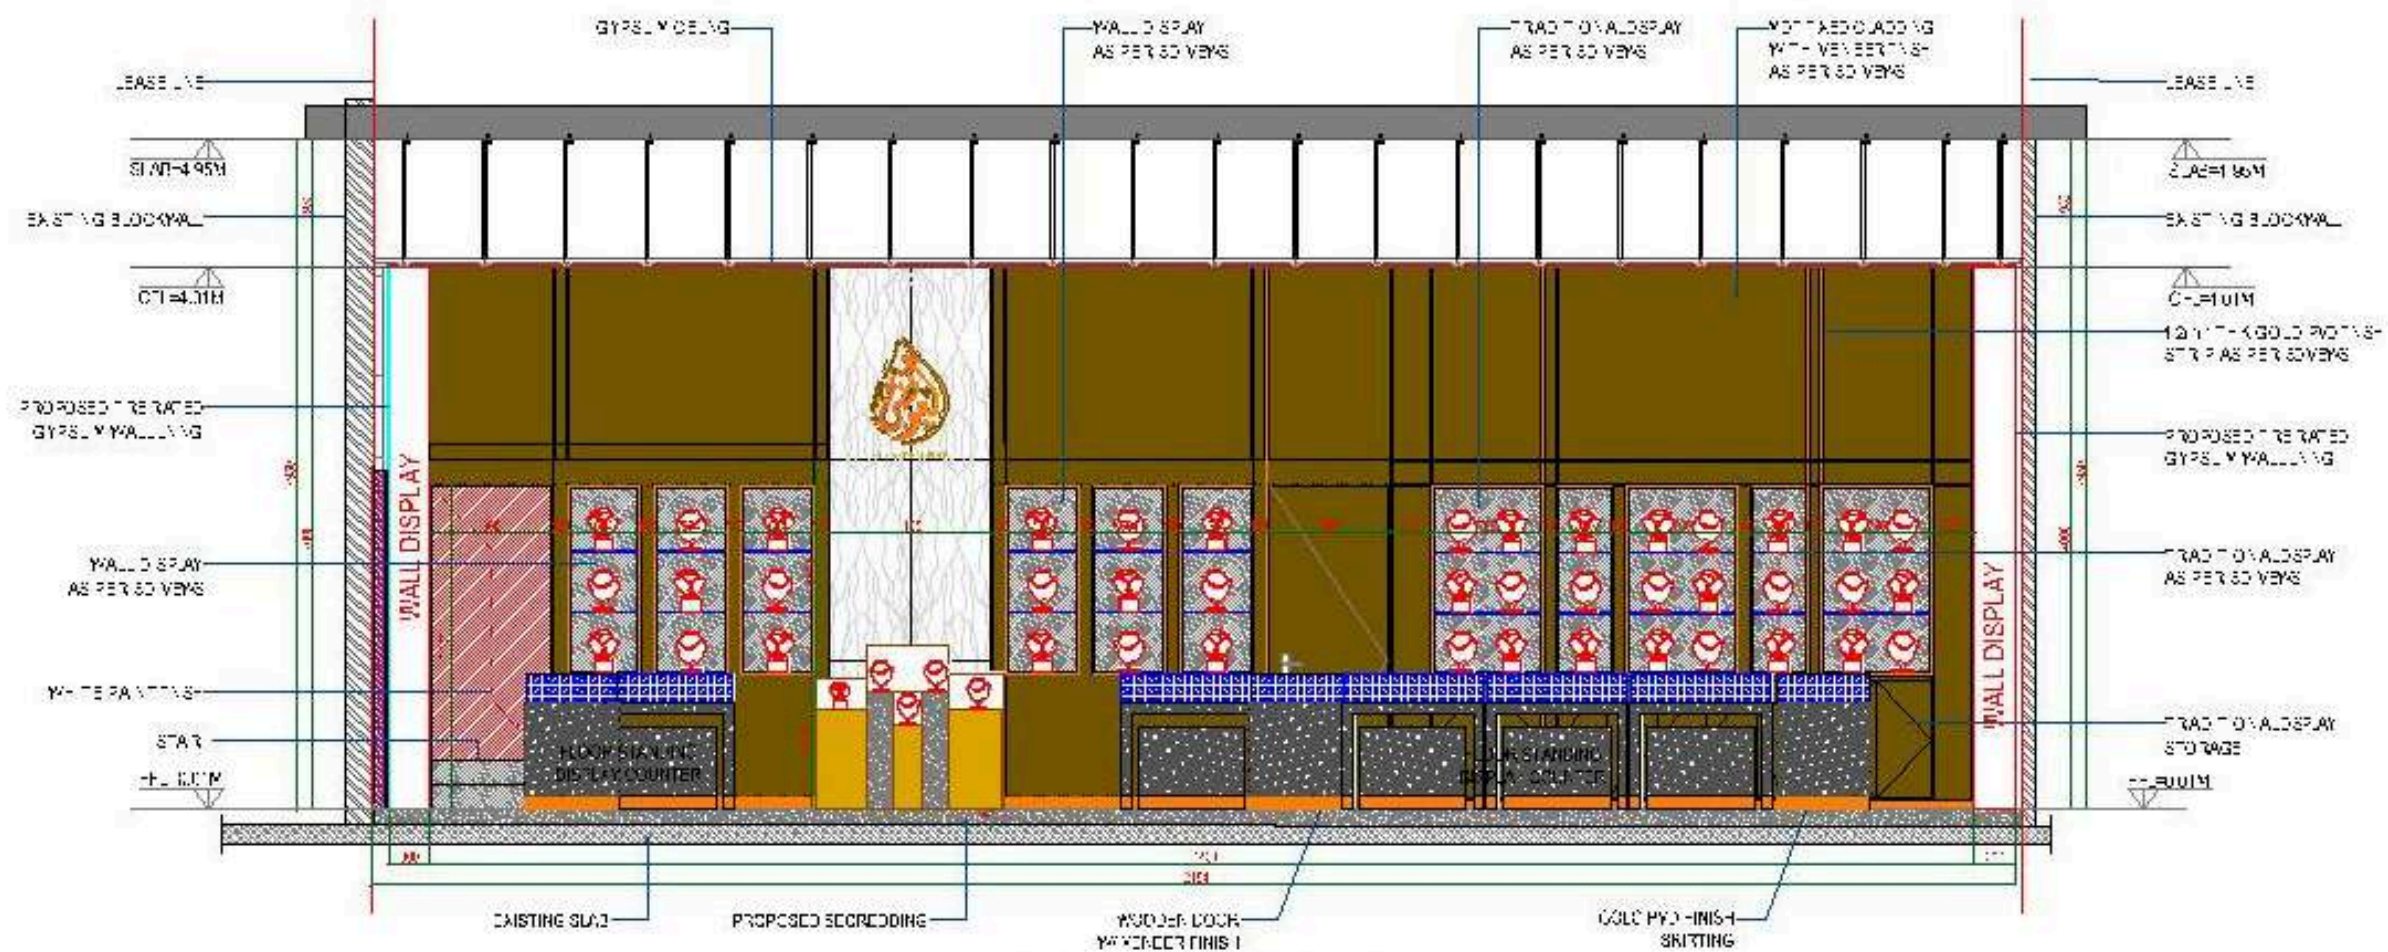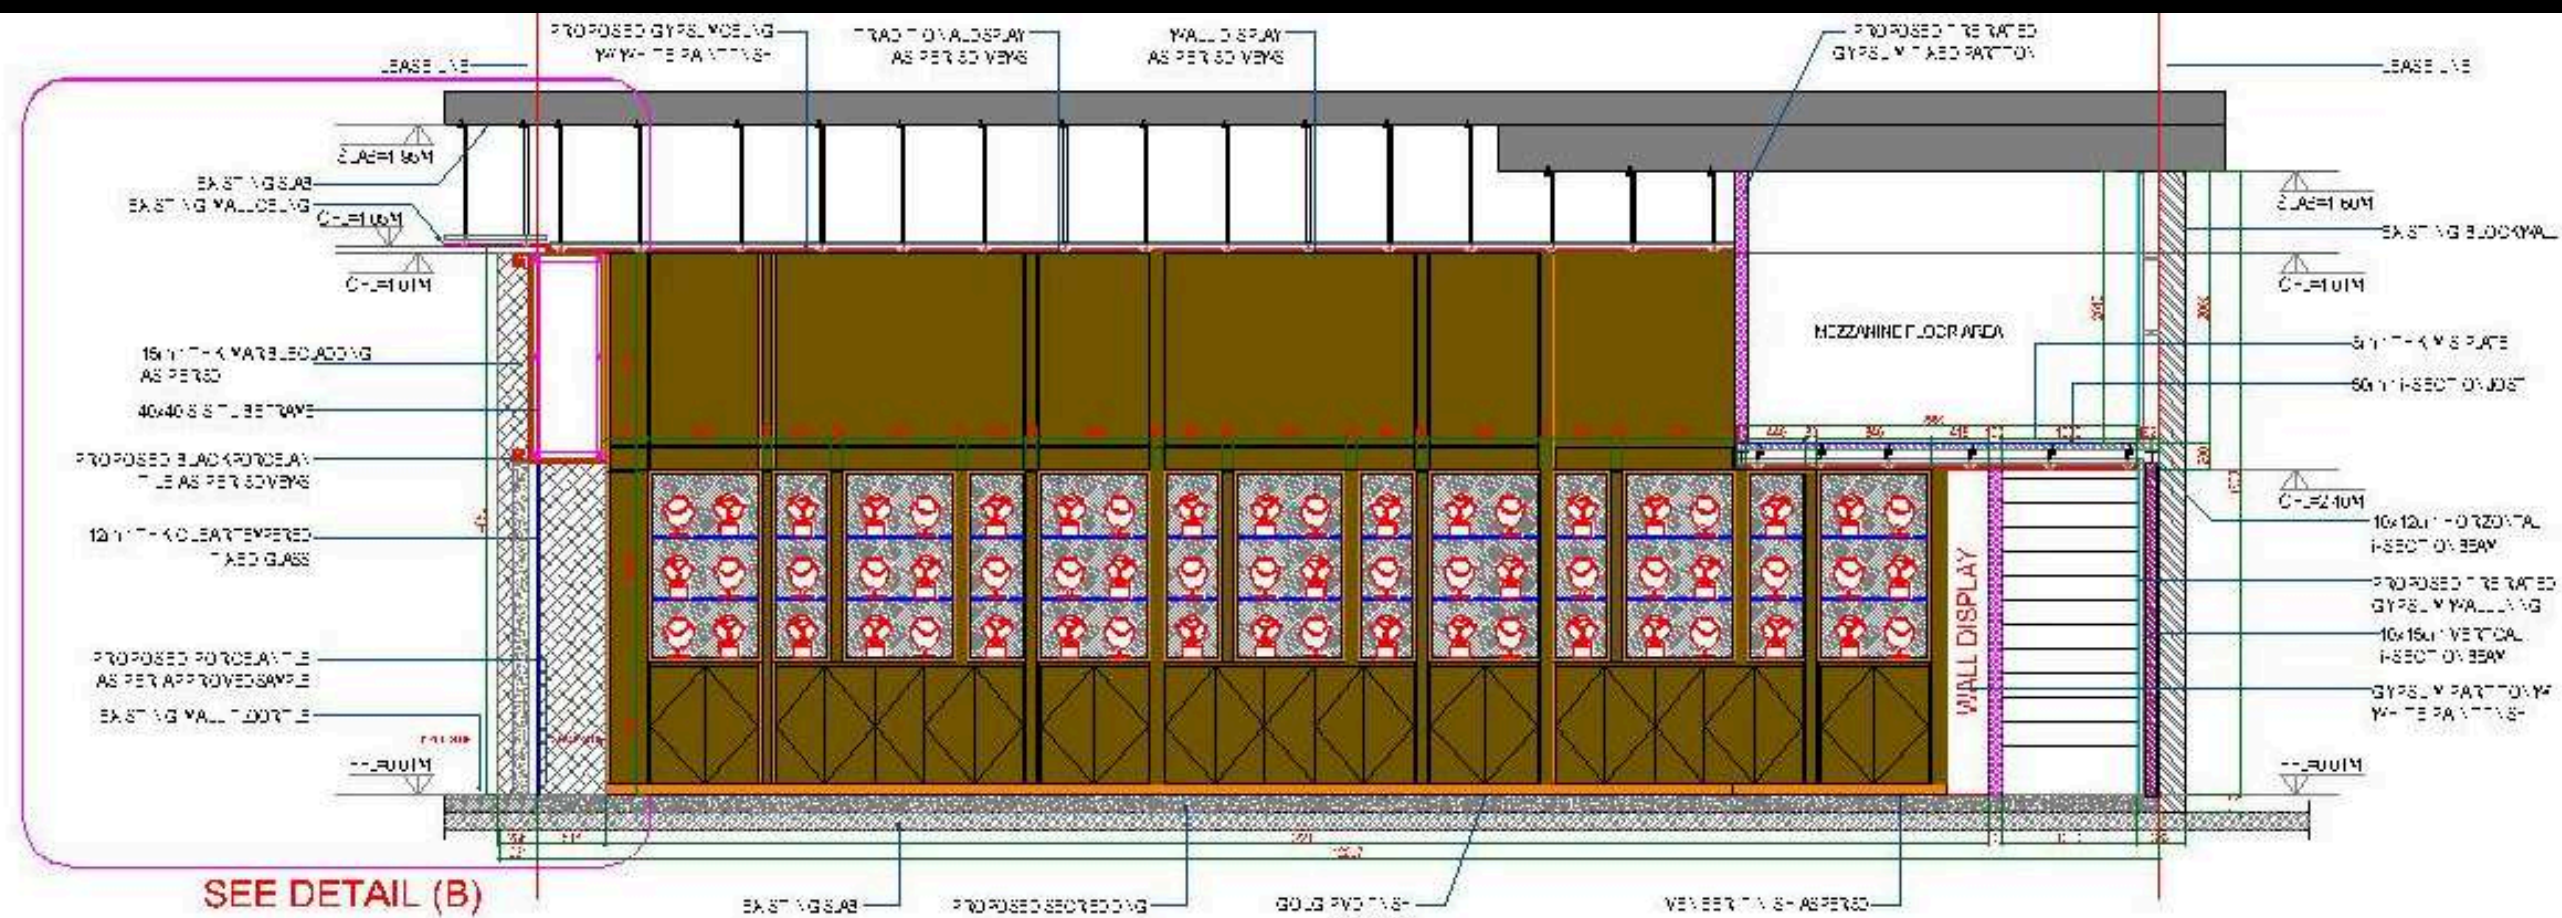










# MAR LOUNGE ABU DHABI

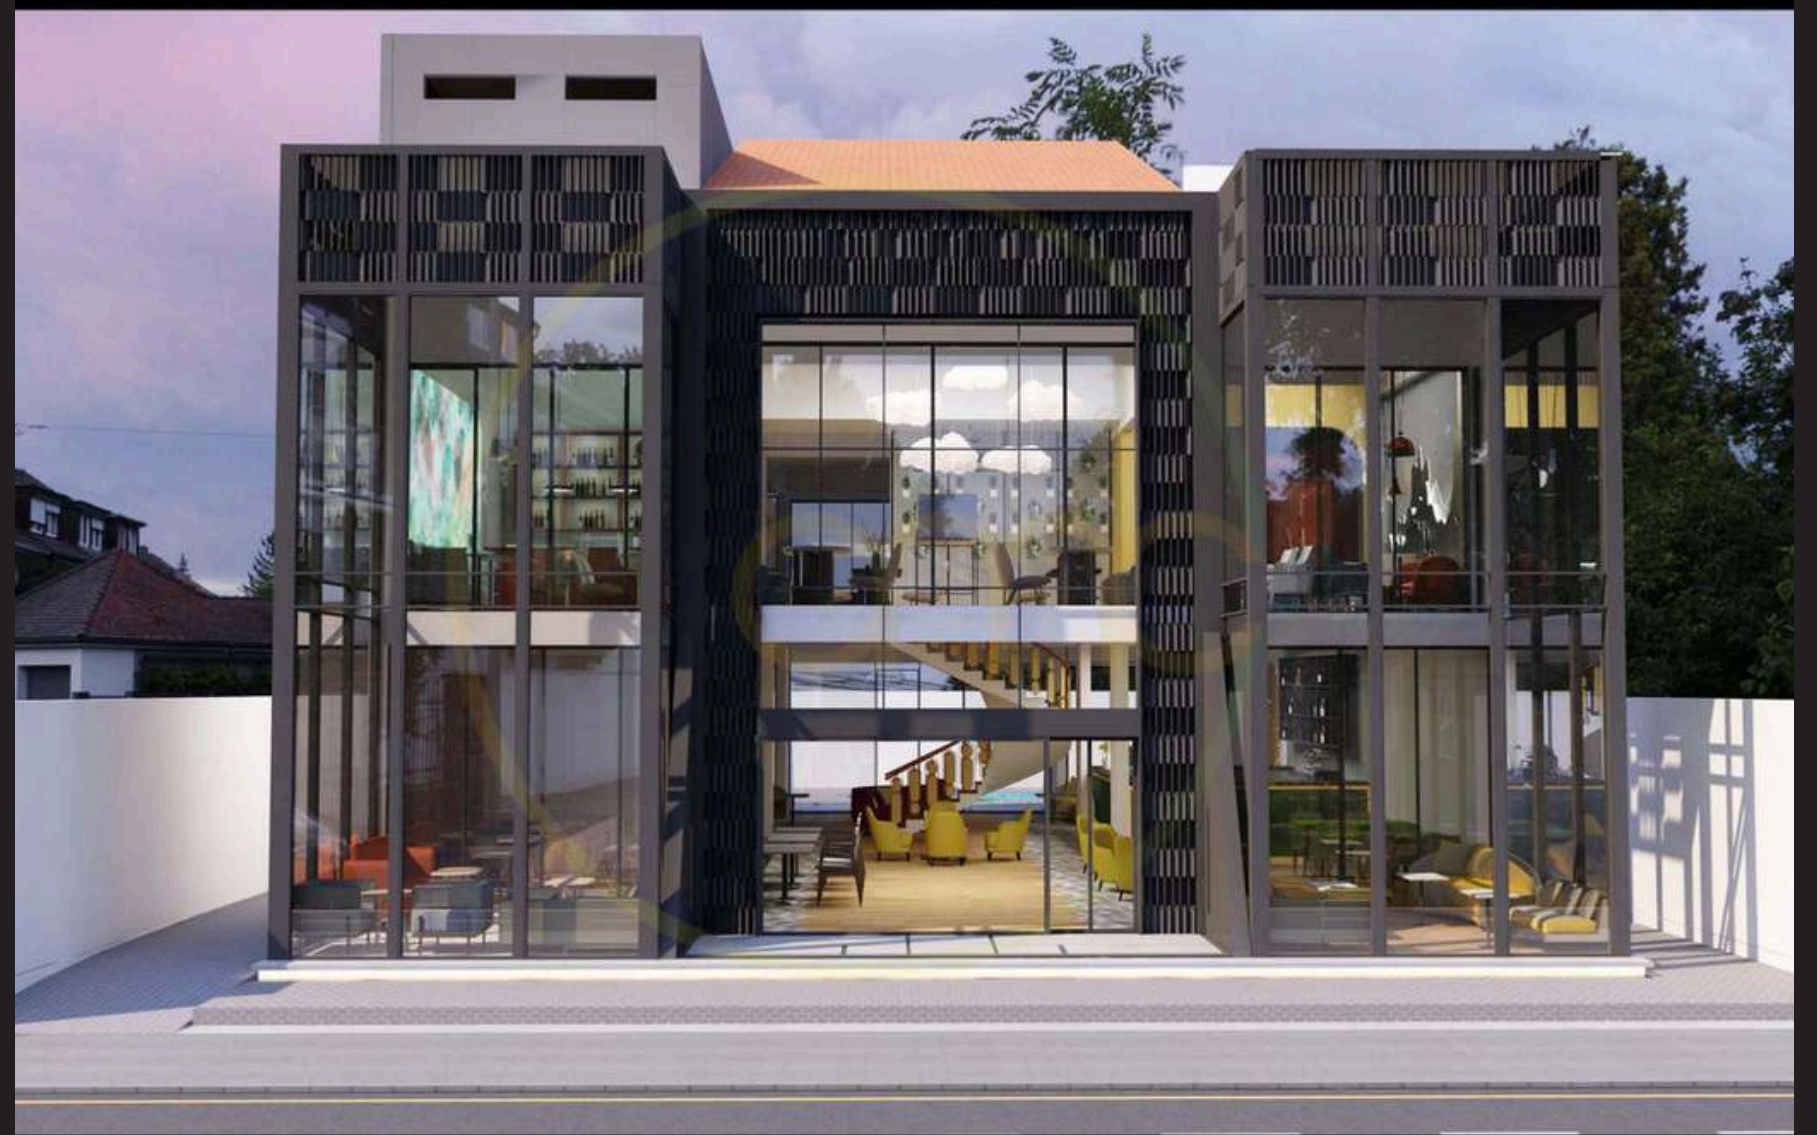




# PROJECT PORTFOLIO

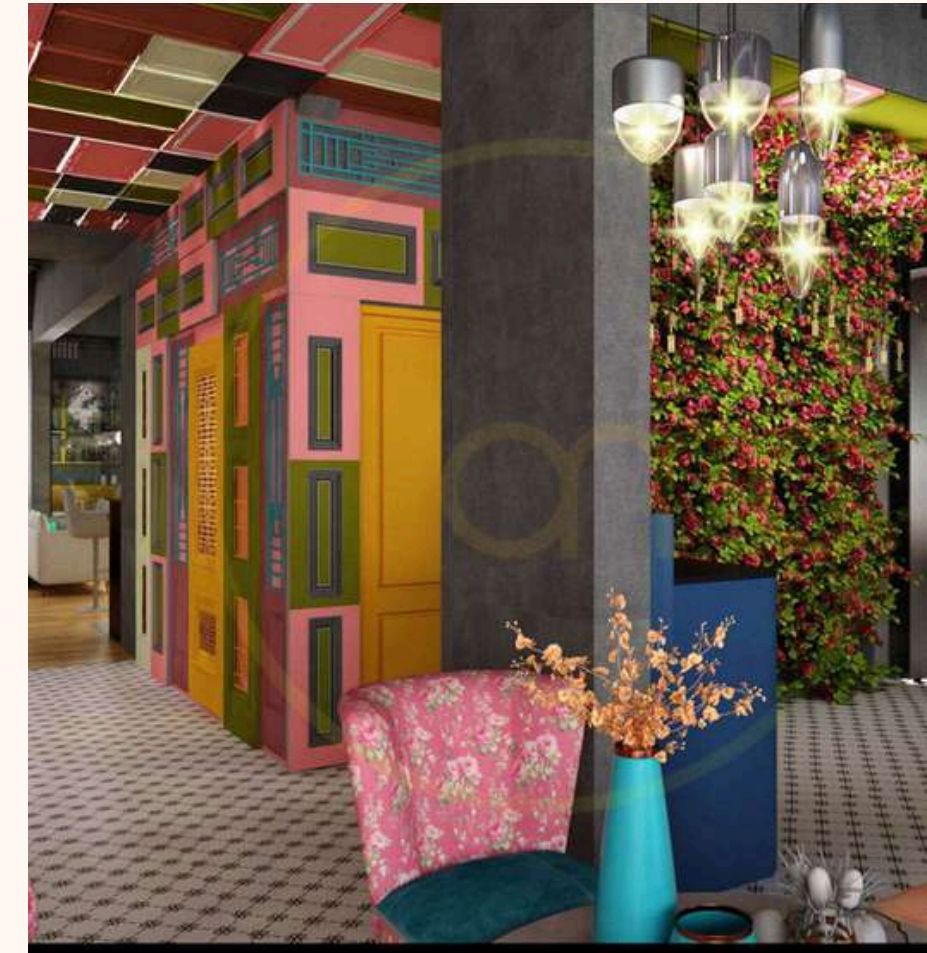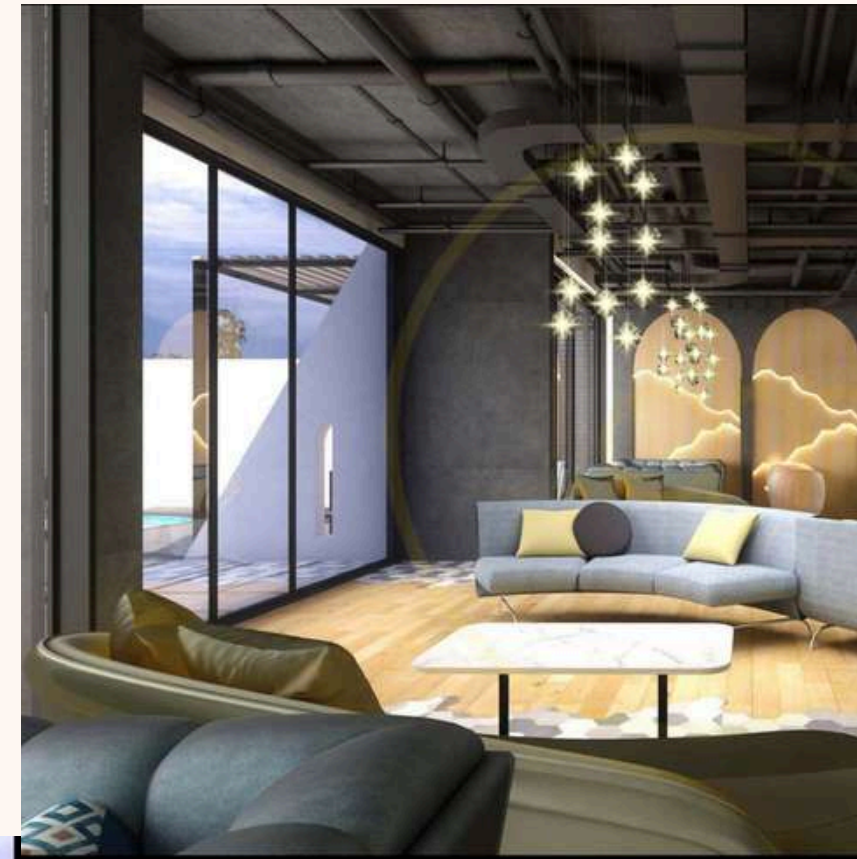

## MAR LOUNGE!

Its a renovation project which is getting convertible from a residential into a commercial coffee and confectionery restaurant the place is consist of 3 floors along with pool side swimming pool.

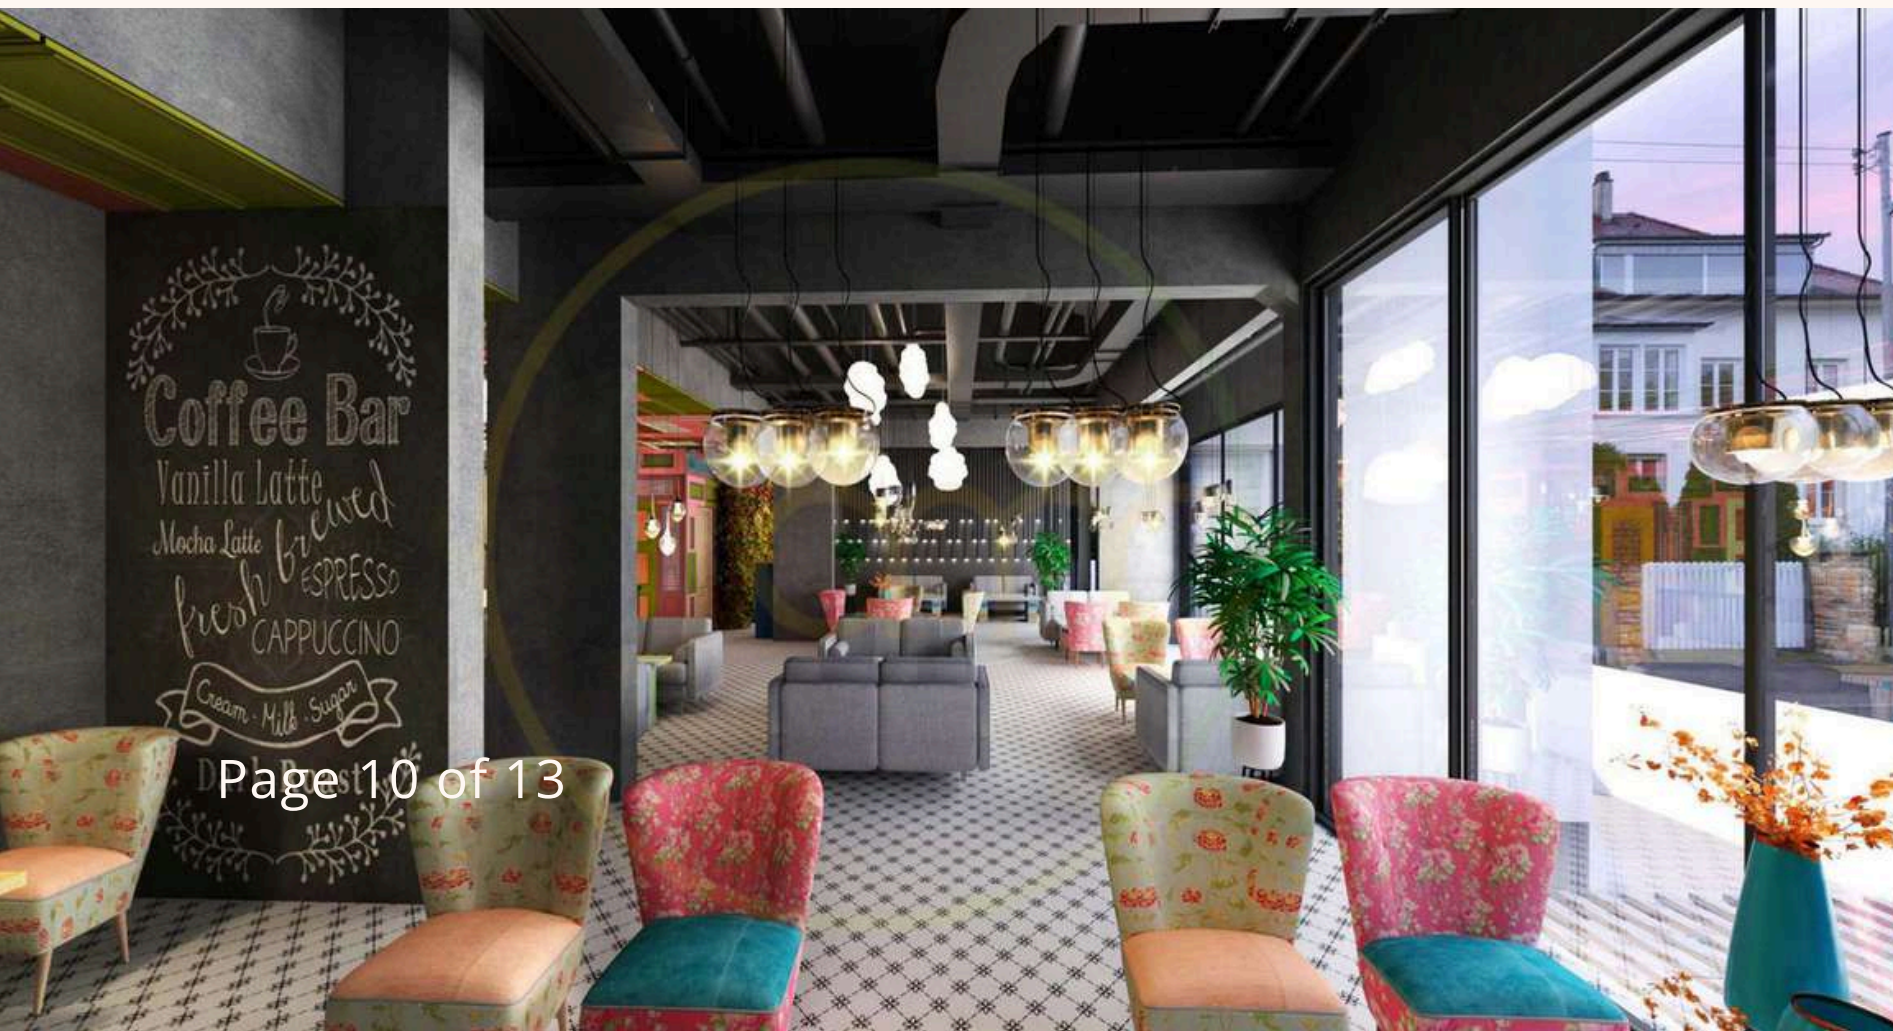



# Creative Portfolio

Shweta Paul Verma






# VILLA 17 ABU DHABI





# PROJECT PORTFOLIO

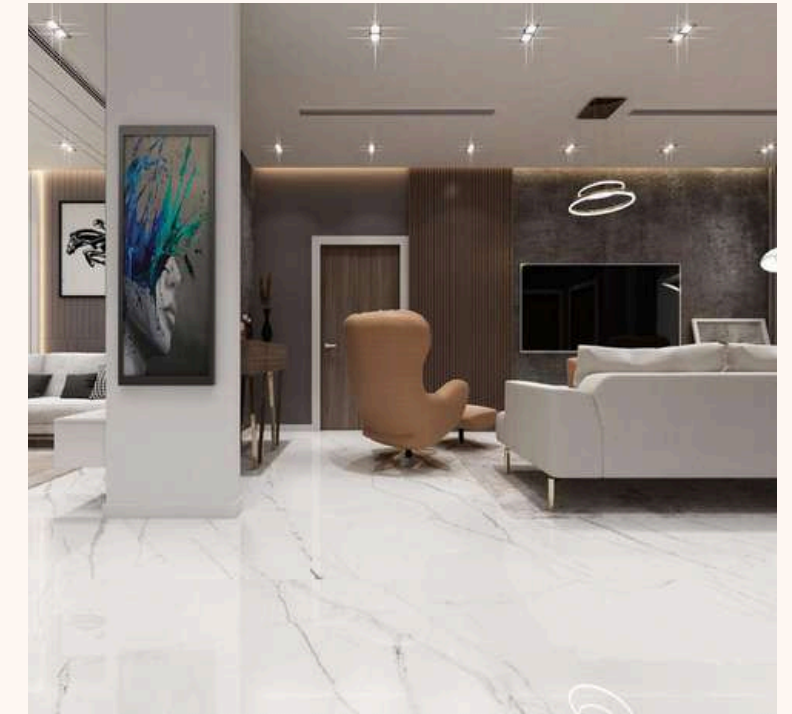


Villa 17!

wow what a place is this.

the villa consist of all the amenities which is aesthetically fulfilling all the functionality of the luxury home.





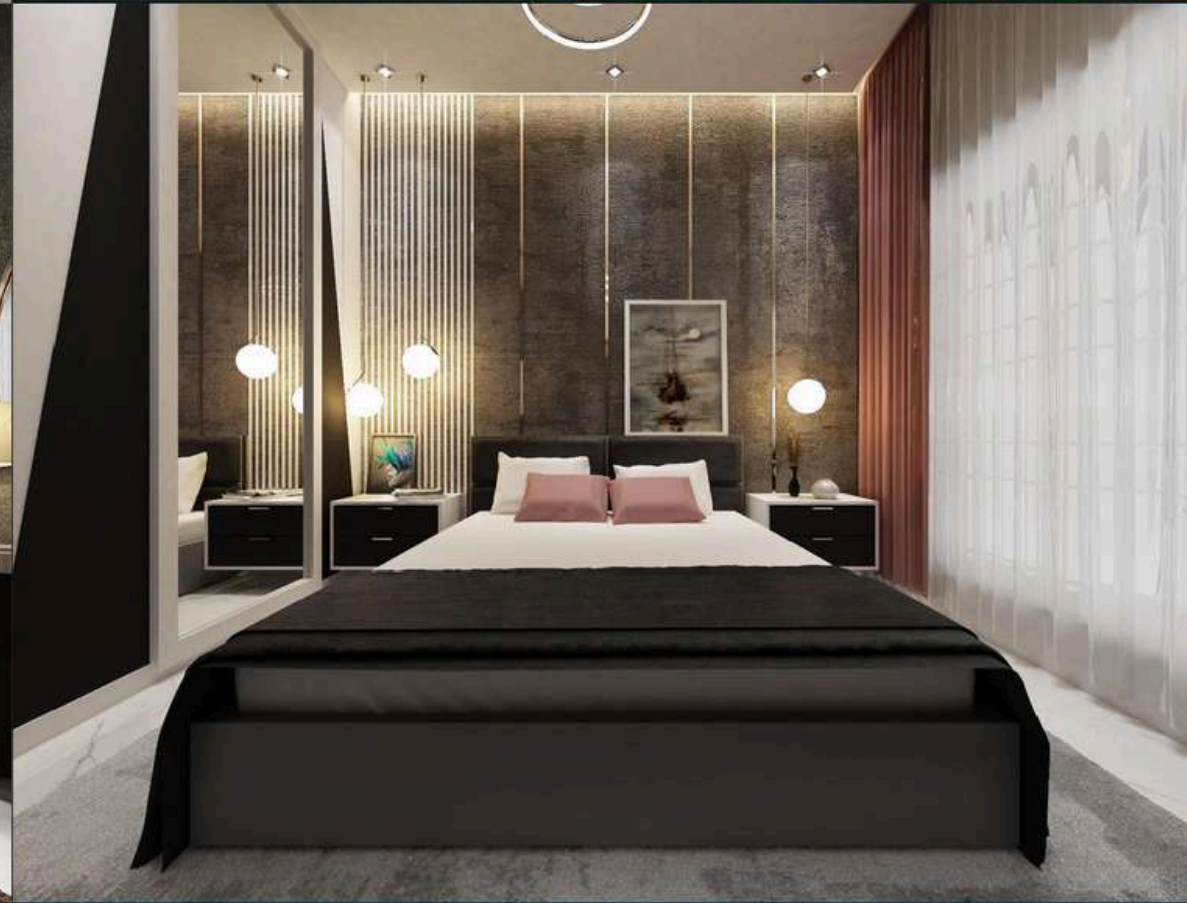



# AL AHWADI JEWELLER ABU DHABI





# PROJECT PORTFOLIO



Al Awadhi Jewelers are based at Al Maqtaa Mall. The place is consist of one floor which is storage and display counter for the jewelry and watches. The mezzanine floor is the place where the backend process will carries out. the shop front is build by the two combinational tile along with glass.






# HANGER LET'S PADEL ABU DHABI






# PROJECT PORTFOLIO

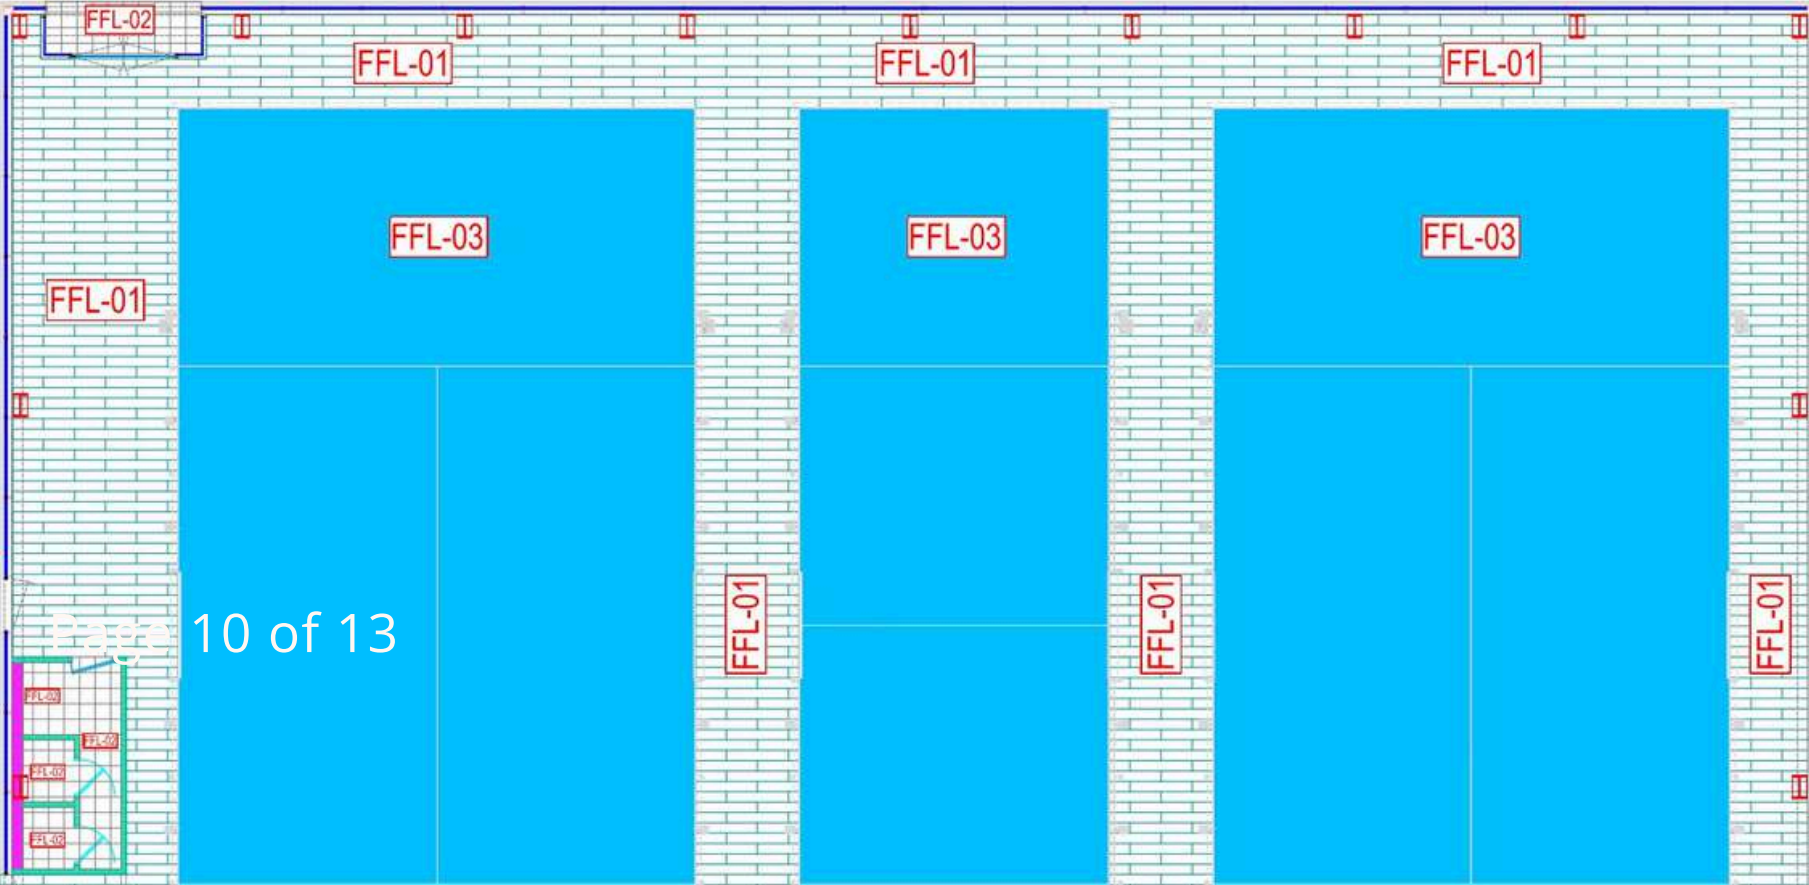

Hanger Let's Padel  
it consists of two dual court and one solo court.  
the place is well equipped with toilets, sitting area and  
reception area.





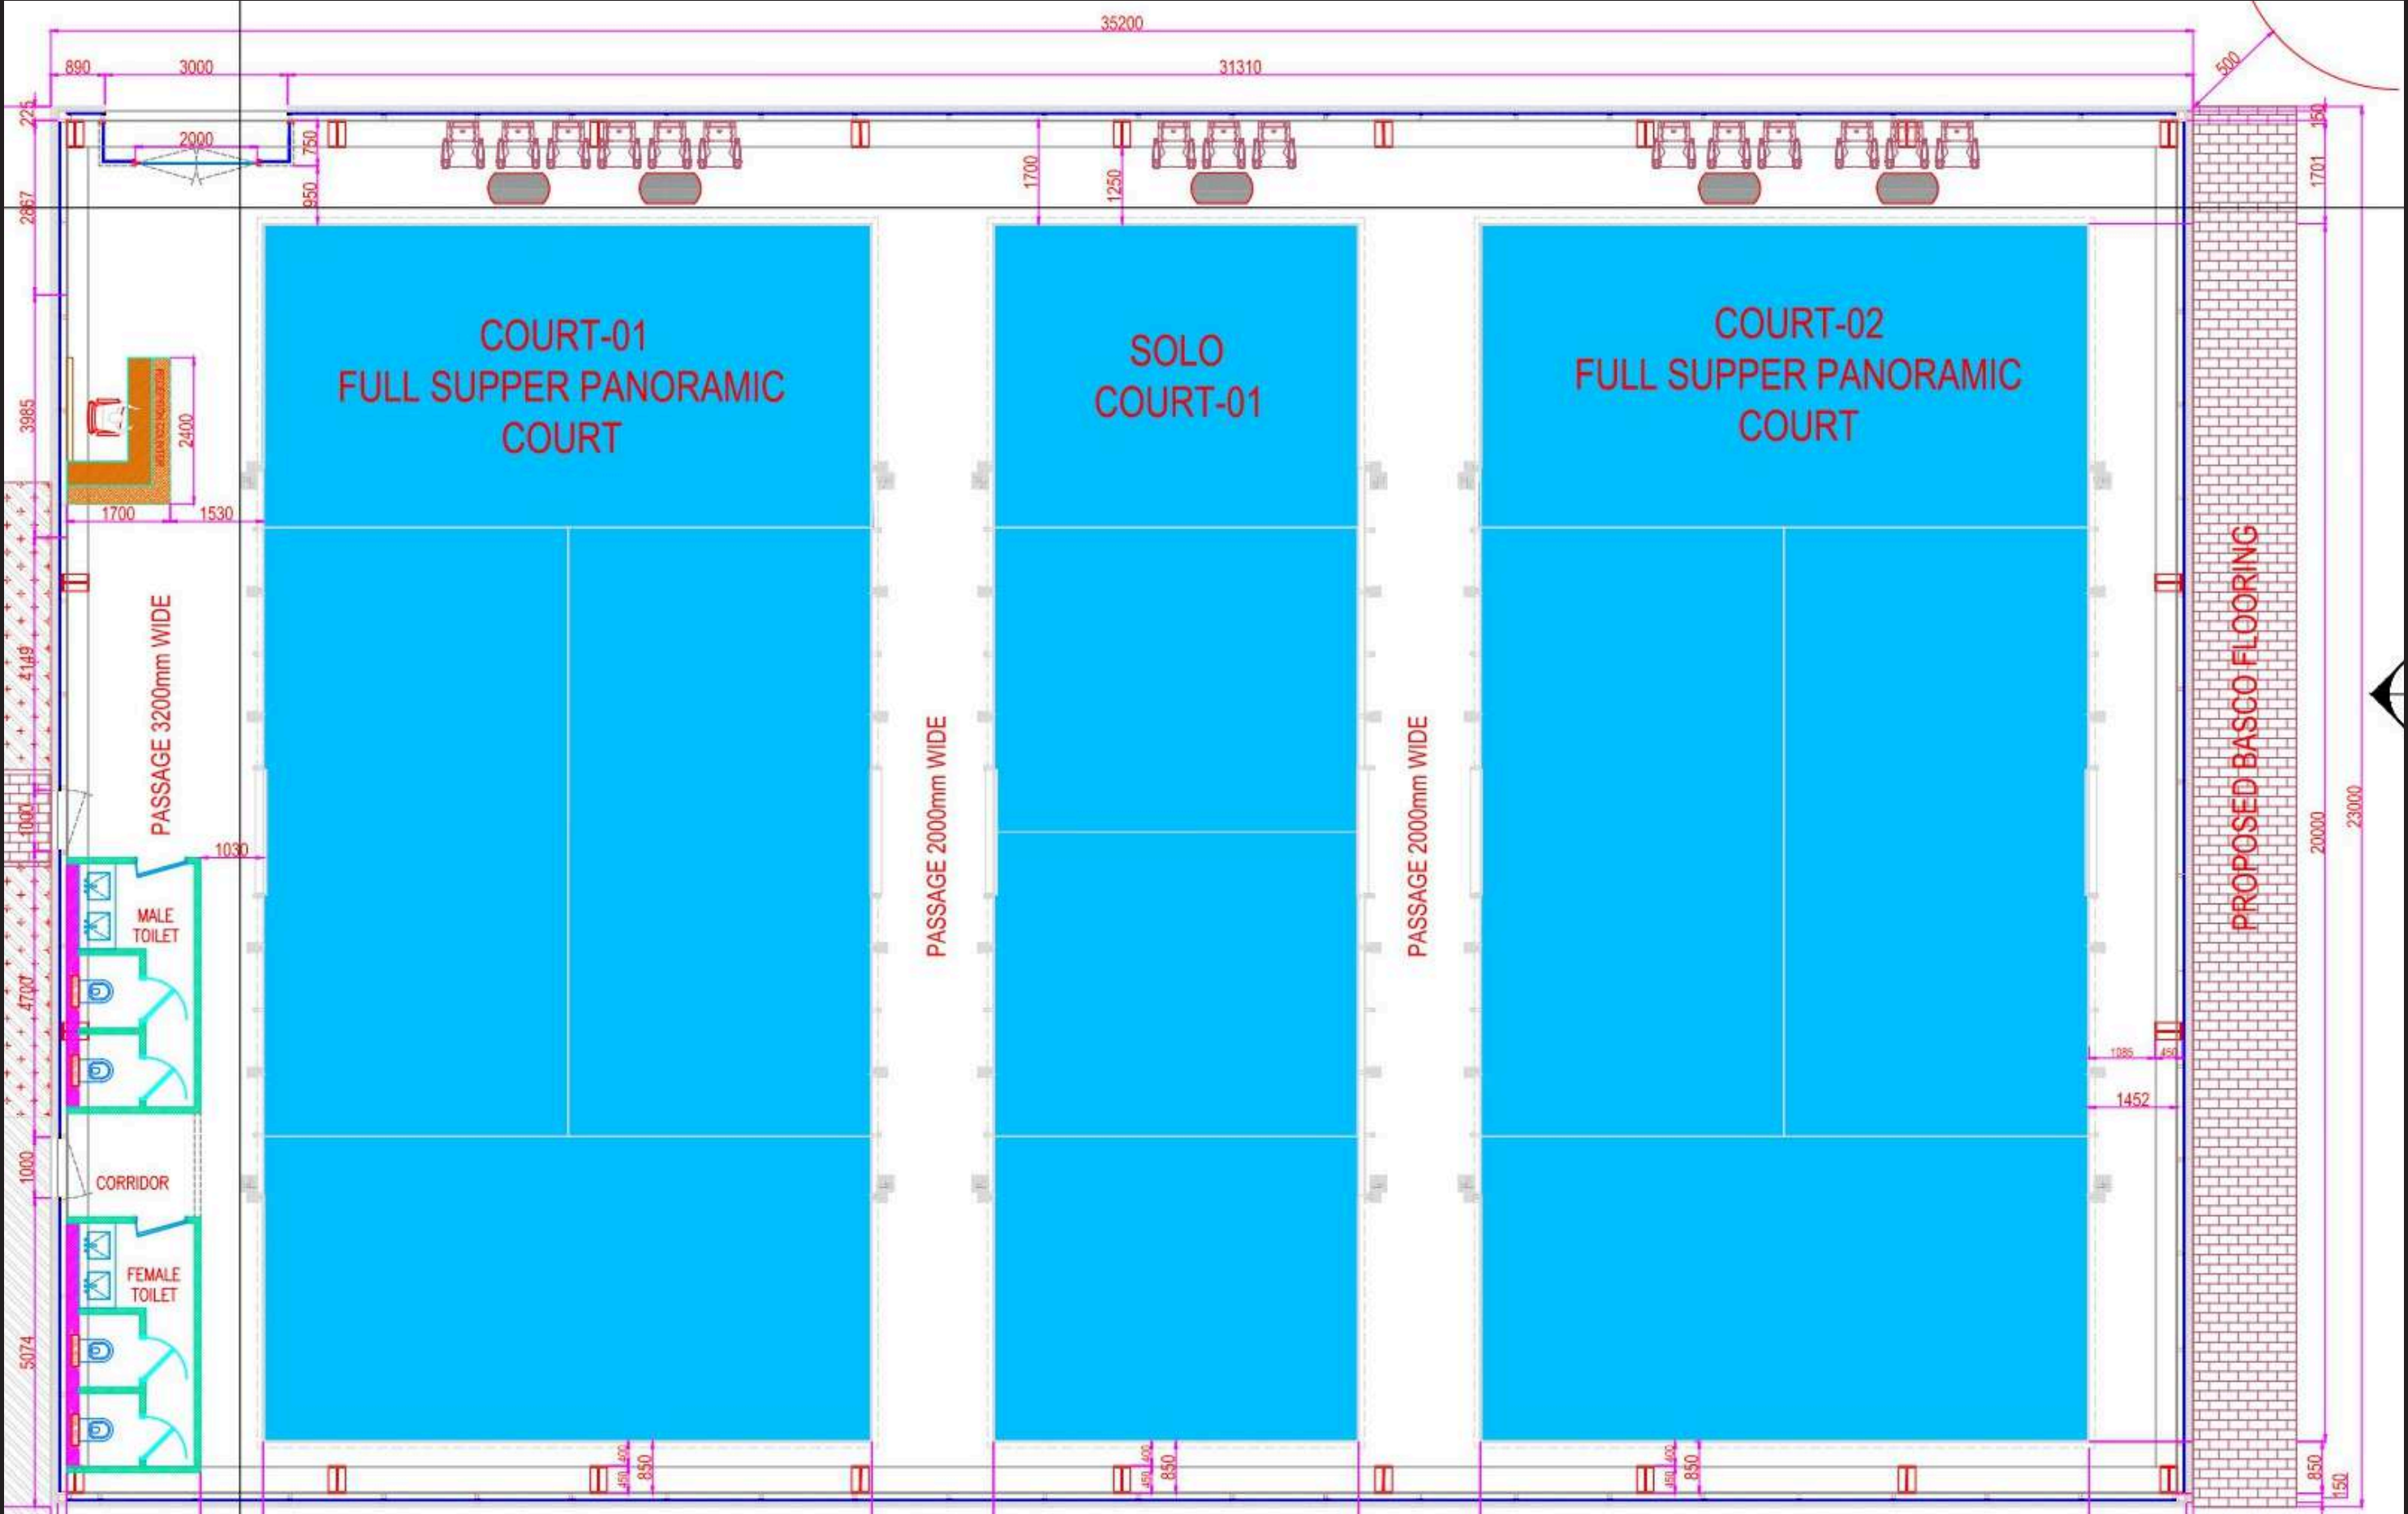



Creative Portfolio

Shweta Paul Verma



Let's work  
**TOGETHER**

---

00971 503083019

shwetapaulverma@gmail.com